


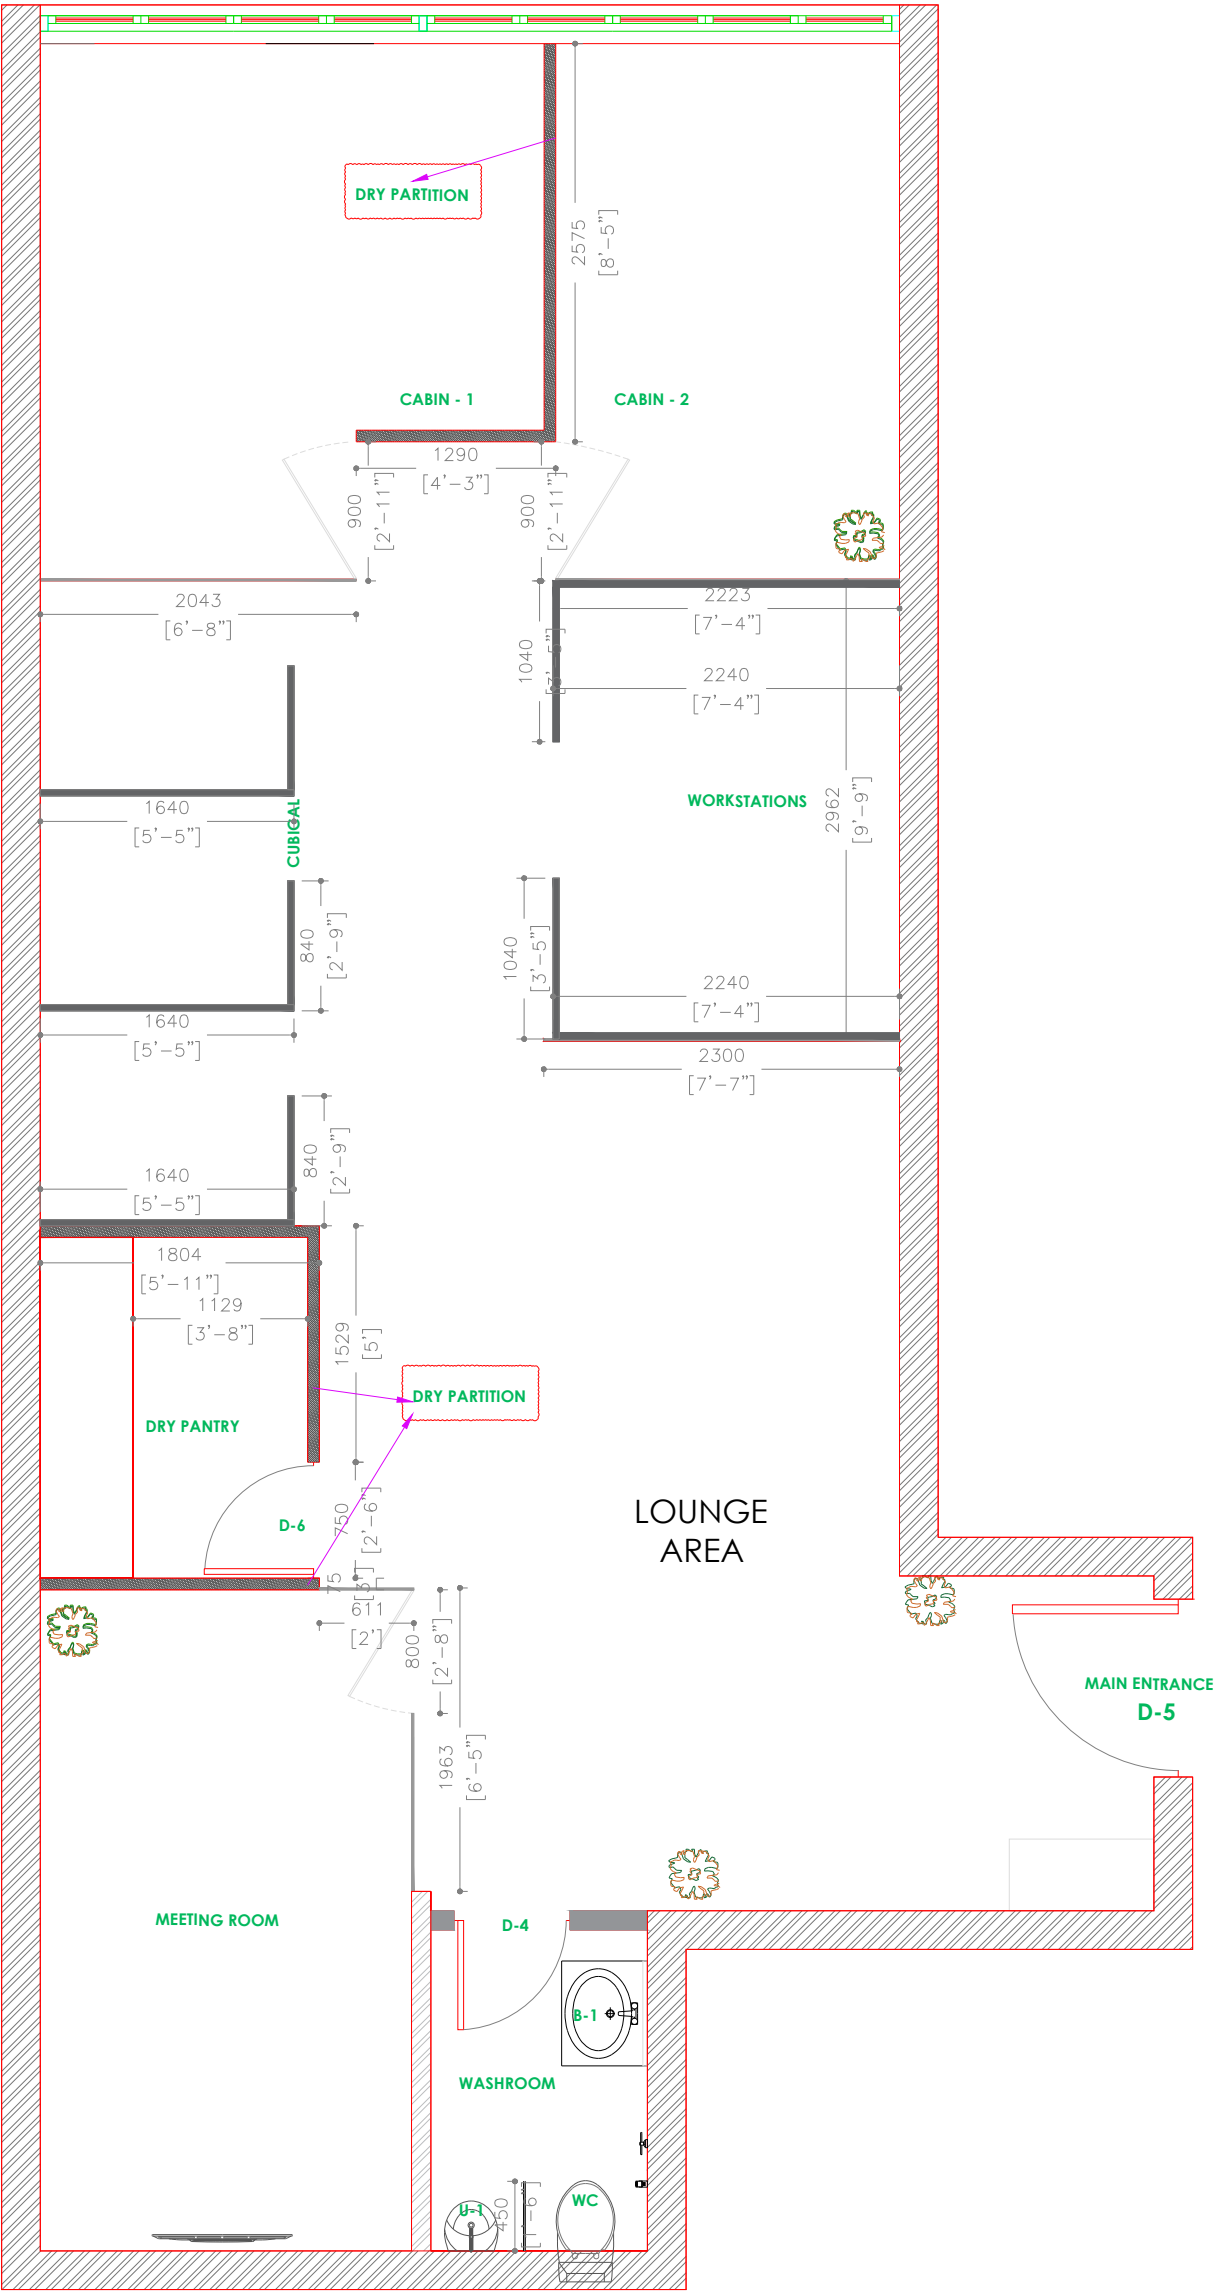

Note: All DIMENSIONS IN MM
Note: All dimensions to be checked on site

DRY PARTITION
GLASS PARTITION
MODULAR PARTITION



PROJECT DETAILS			SITE DETAILS			DRAWING DETAILS			CLIENT	ARCHITECT
Project	RENOVATION WORK		Floor	-		Dwg Status	CIVIL GLAZING LAYOUT	10-03-2026		BIRD ENGINEERING PVT LTD.
Site	E-9 , 2RD FLOOR CP		Floor carpet Area	-	78.98 SQM	Dwg Title	INTERNAL LAYOUT	POOJA DAKSH		
Address	E-9, Connaught House, CP, New Delhi, 11001		B.O.Slab	-		Dwg No.	5	ABHISHEK DWIVEDI		
			B.O.Beam	-		Scale	Fit to paper			
Channel P	-		B.O.F.Ceiling	-		All the dimensions in millimeter				