
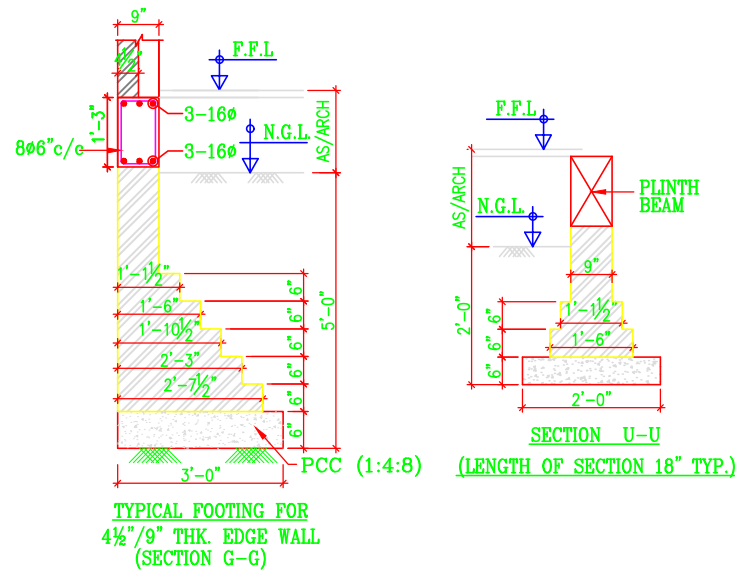
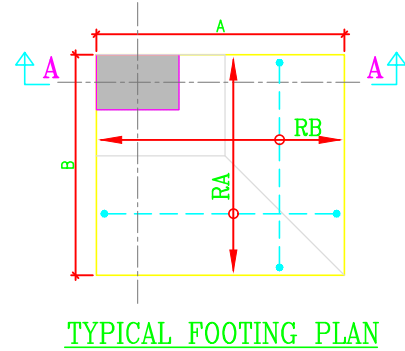
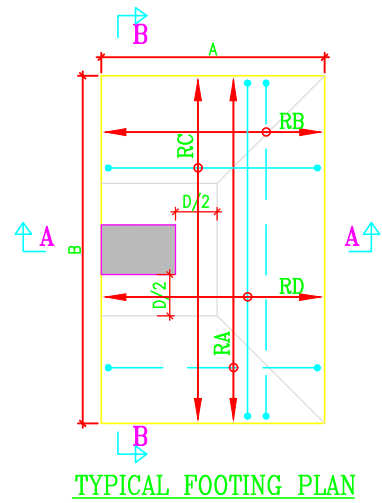
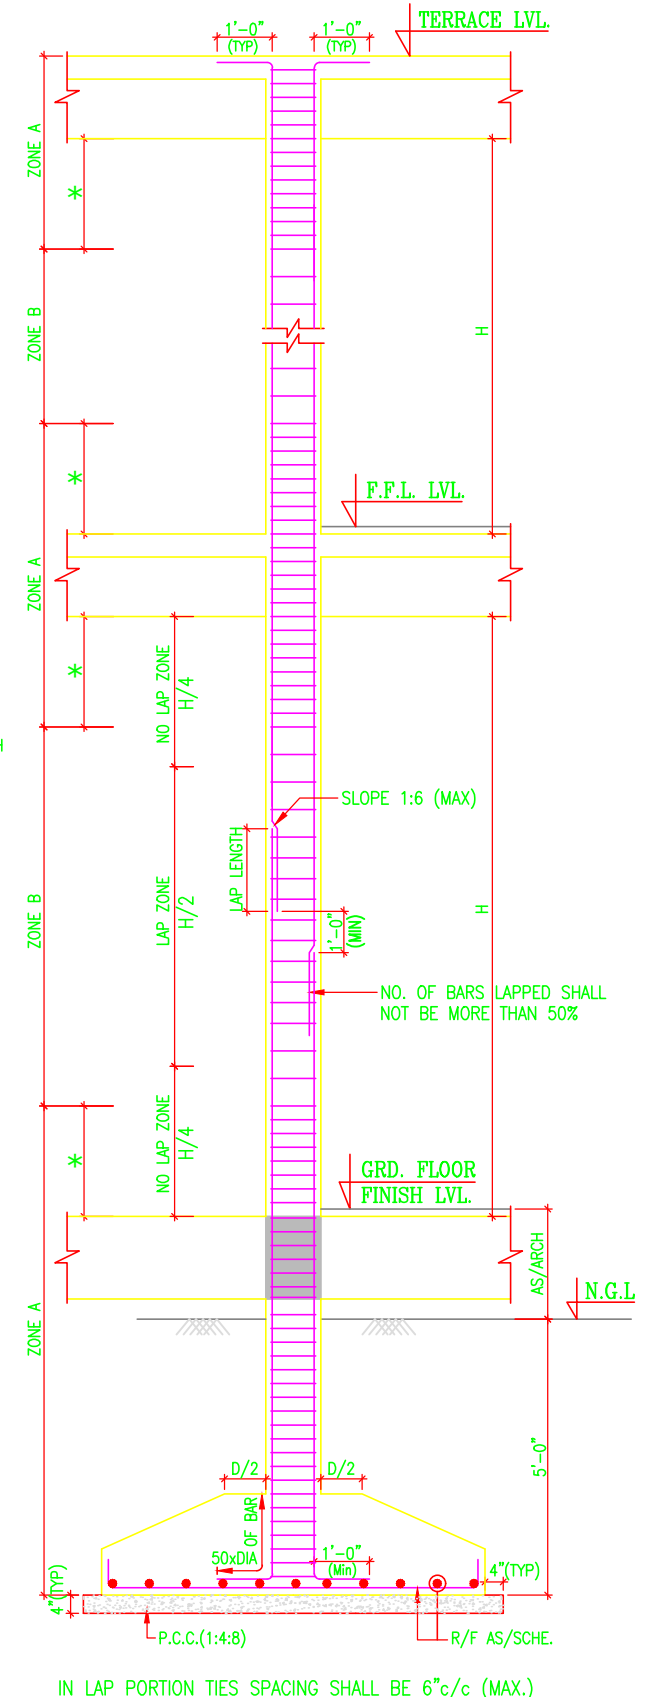
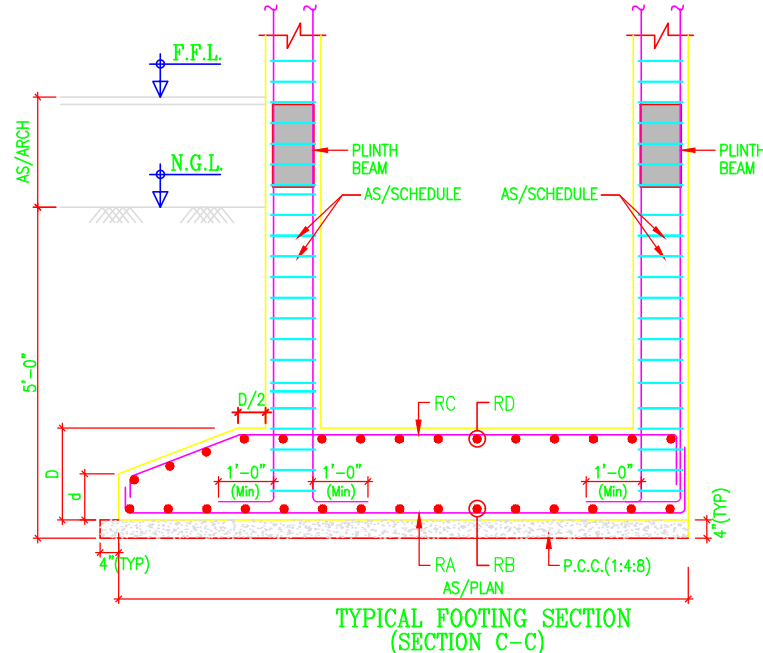
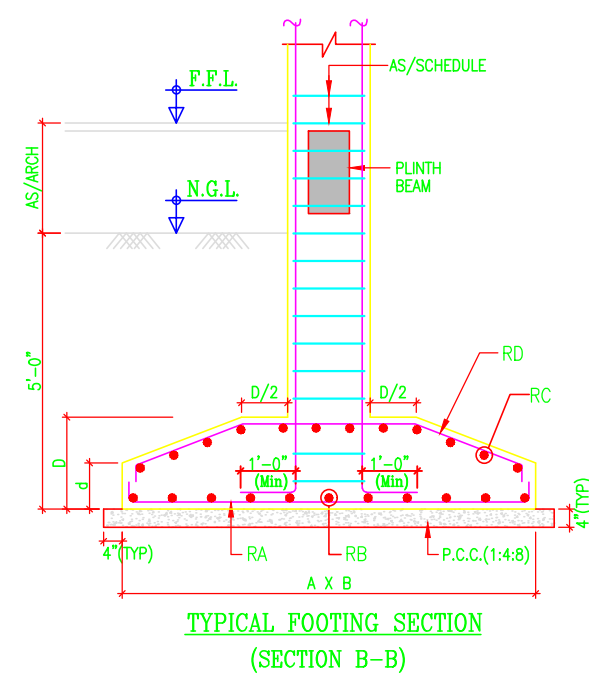


LAP LENGTH FOR
Fe-550 & M-25

DIA OF BAR	LENGTH OF BAR
25	4'-2"
20	3'-4"
16	2'-8"
12	2'-0"
10	1'-8"
8	1'-4"

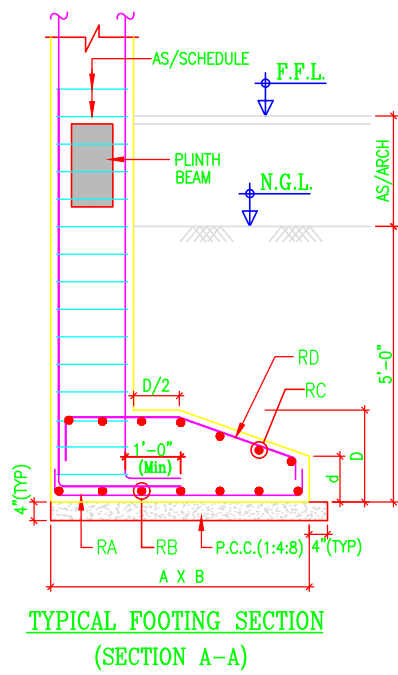


COLUMN SCHEDULE

COL. MARK	COLUMN SIZE	FOUNDATION REINFORCEMENT	TIES
C1	1'-0" x 1'-0"	A= 4-16# B= 4-16#	Y, X
C2	1'-3" x 1'-3"	A= 4-16# B= 4-16#	Y, X
C3	1'-6" x 1'-6"	A= 4-16# B= 4-16# C= 2-16#	Y, X, Y
C4	1'-6" x 1'-6"	A= 4-20# B= 4-20# C= 2-20#	Y, X, Y



FOOTING SCHEDULE

FOOTING MARK	DIMENSIONS		DEPTH		BOTTOM REINFORCEMENT		TOP REINFORCEMENT		REFER SECTION
	A	B	D	d	RA	RB	RC	RD	
F1	5'-3"	5'-3"	22"	10"	12#@4"c/c	12#@4"c/c	----	----	A-A
F2	6'-9"	7'-3"	28"	10"	12#@3 1/2"c/c	12#@3 1/2"c/c	----	----	A-A
F3	5'-6"	11'-0"	26"	10"	12#@4"c/c	12#@4"c/c	----	----	B-B
F4	5'-9"	8'-0"	28"	10"	12#@3 1/2"c/c	12#@3 1/2"c/c	----	----	A-A
F5	5'-10"	10'-4"	26"	10"	12#@4"c/c	12#@4"c/c	----	----	B-B
CF1	10'-0"	12'-6"	22"	10"	12#@4"c/c	12#@4"c/c	10#@5"c/c	10#@5"c/c	C-C
CF2	8'-3"	12'-8"	22"	10"	12#@4"c/c	12#@4"c/c	10#@6"c/c	10#@6"c/c	C-C
CF3	6'-3"	13'-5"	26"	10"	12#@4"c/c	12#@4"c/c	10#@4"c/c	10#@4"c/c	C-C

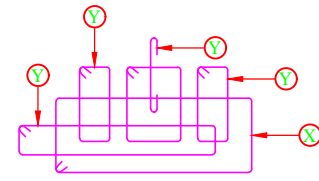

TIES GROUP SCHEDULE

ZONE	TIES	TIES	
		RA	RB
ZONE (A)	X	10#@4"c/c	8#@4"c/c
ZONE (B)	Y	10#@8"c/c	8#@8"c/c

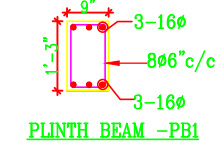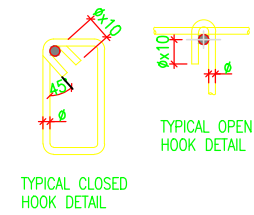

* H/6
OR LARGEST DIM. OF
COLUMN OR 18"
WHICHEVER IS MAXIMUM.