


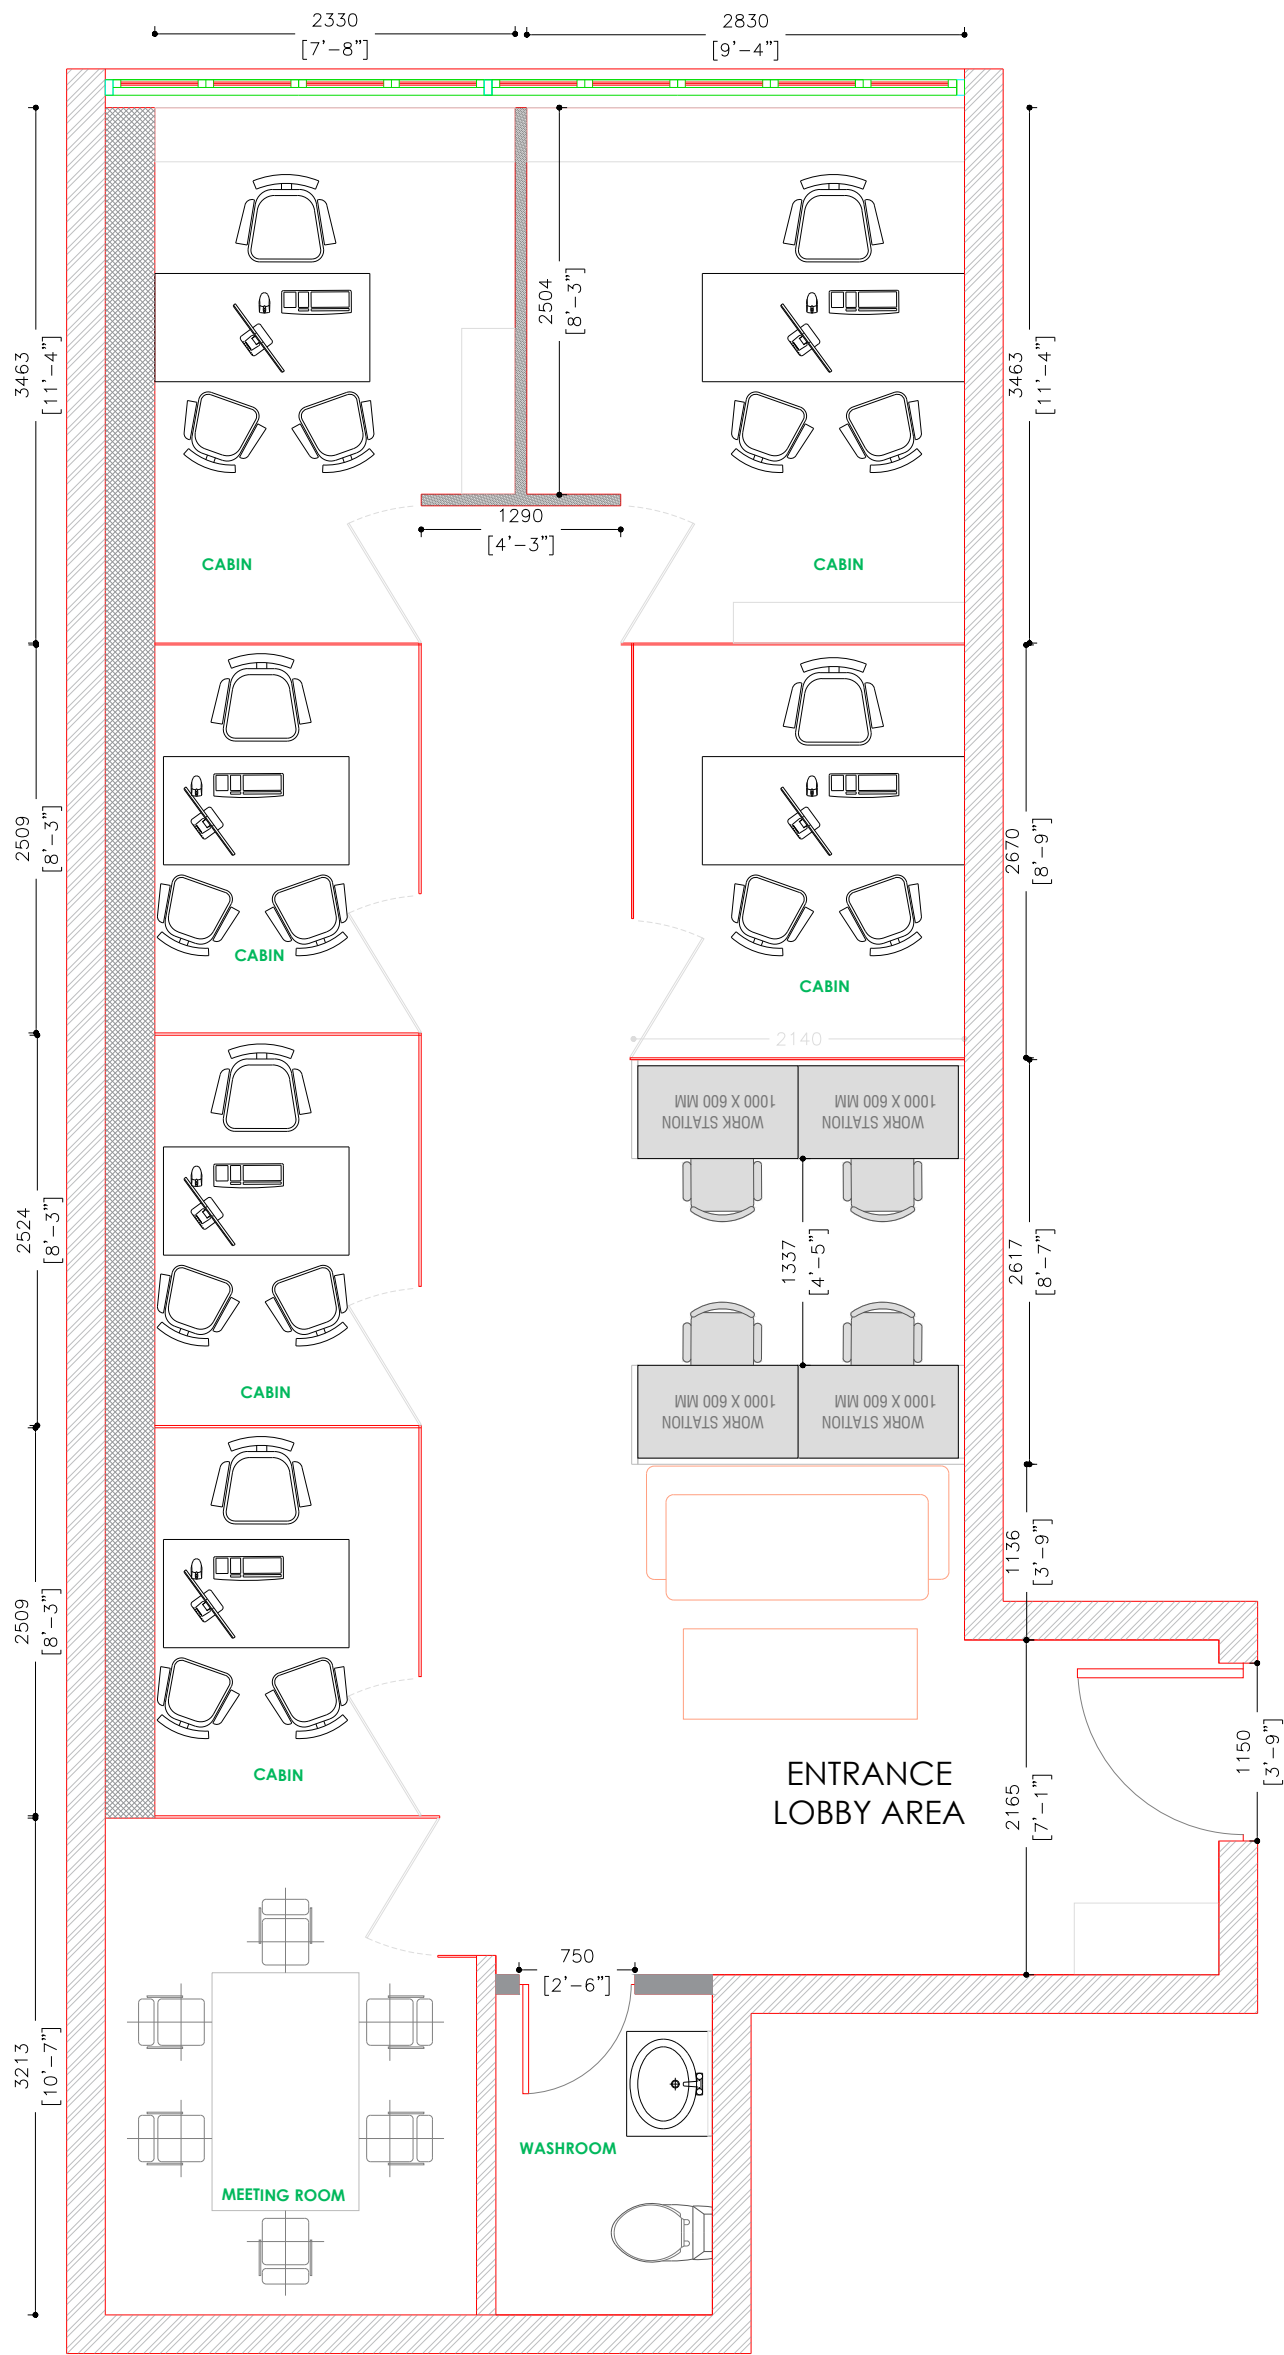


Note: All DIMENSIONS IN MM

Note: All dimensions to be checked on site



PROJECT DETAILS		SITE DETAILS		DRAWING DETAILS				CLIENT	ARCHITECT
Project	RENOVATION WORK	Floor	-	Dwg Status	EXISTING LAYOUT		Date	03-03-2026	BIRD ENGINEERING PVT LTD.
Site	E-9 , 2RD FLOOR CP	Floor carpet Area	- 78.98 SQM	Dwg Title	INTERNAL LAYOUT		Dwn by	POOJA DAKSH	
Address	E-9, Connaught House, CP, New Delhi, 11001	B.O.Slab	-	Dwg No.	1		Chk By	ABHISHEK DWIVEDI	
Channel P	-	B.O.Beam	-	Scale	Fit to paper				
		B.O.F.Ceiling	-	All the dimensions in millimeter					

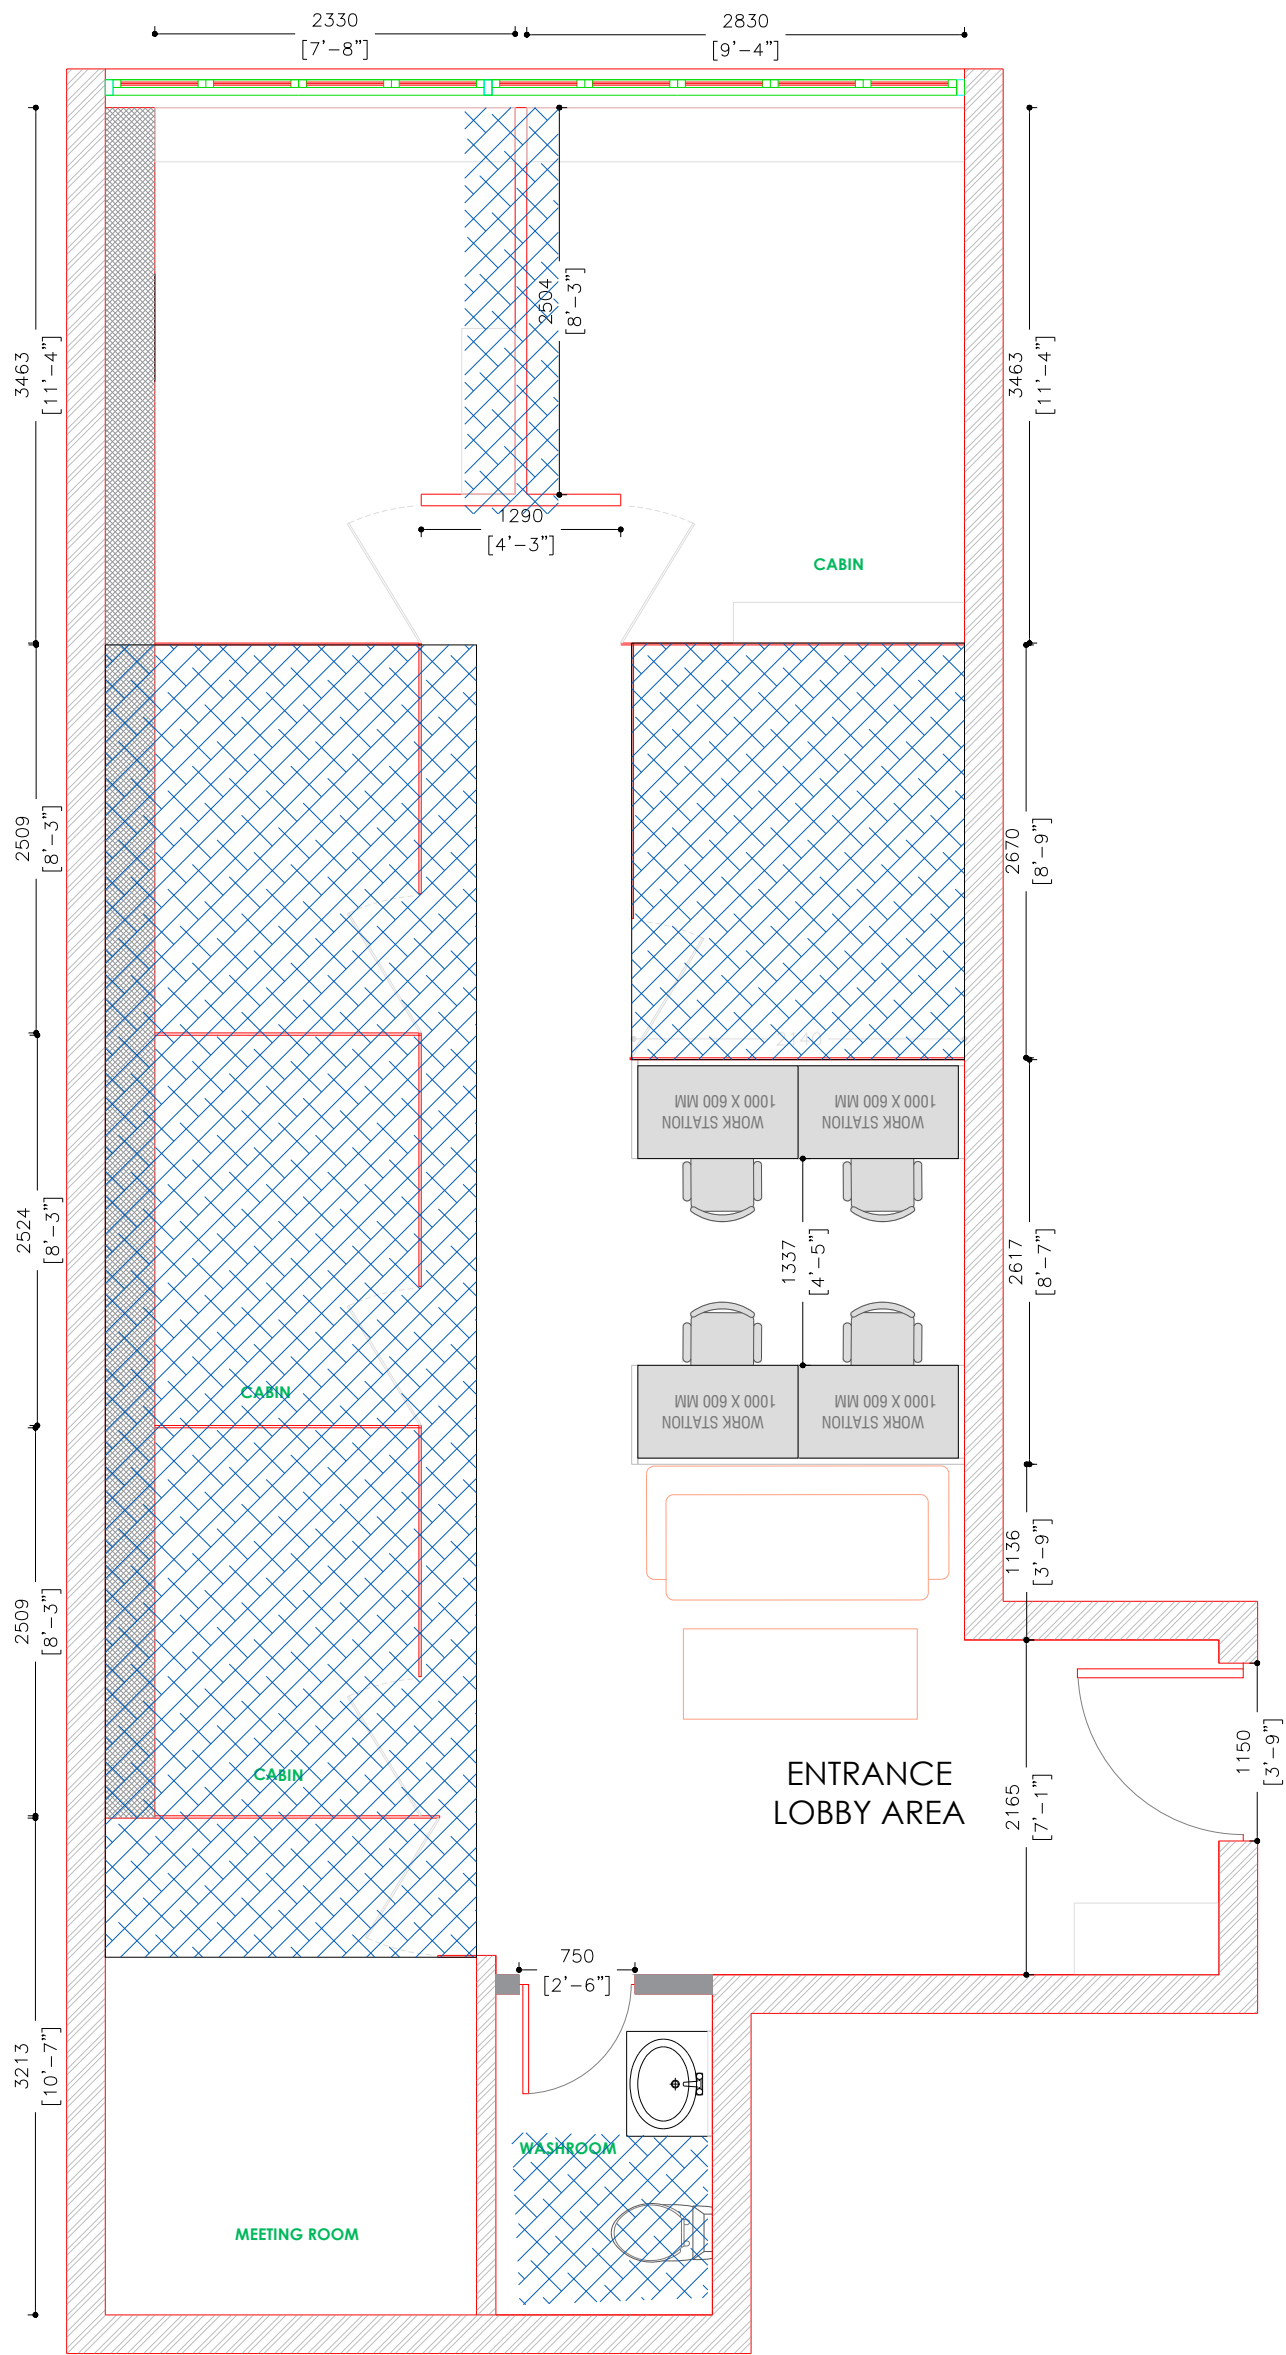


Note: All DIMENSIONS IN MM

Note: All dimensions to be checked on site



PROJECT DETAILS		SITE DETAILS		DRAWING DETAILS				CLIENT	ARCHITECT
Project	RENOVATION WORK	Floor	-	Dwg Status	DISMANTLING LAYOUT	Date	03-03-2026		BIRD ENGINEERING PVT LTD.
Site	E-9 , 2RD FLOOR CP	Floor carpet Area	- 78.98 SQM	Dwg Title	INTERNAL LAYOUT	Dwn by	POOJA DAKSH		
Address	E-9, Connaught House, CP, New Delhi, 11001	B.O.Slab	-	Dwg No.	2	Chk By	ABHISHEK DWIVEDI		
Channel P	-	B.O.Beam	-	Scale	Fit to paper				
		B.O.F.Ceiling	-	All the dimensions in millimeter					

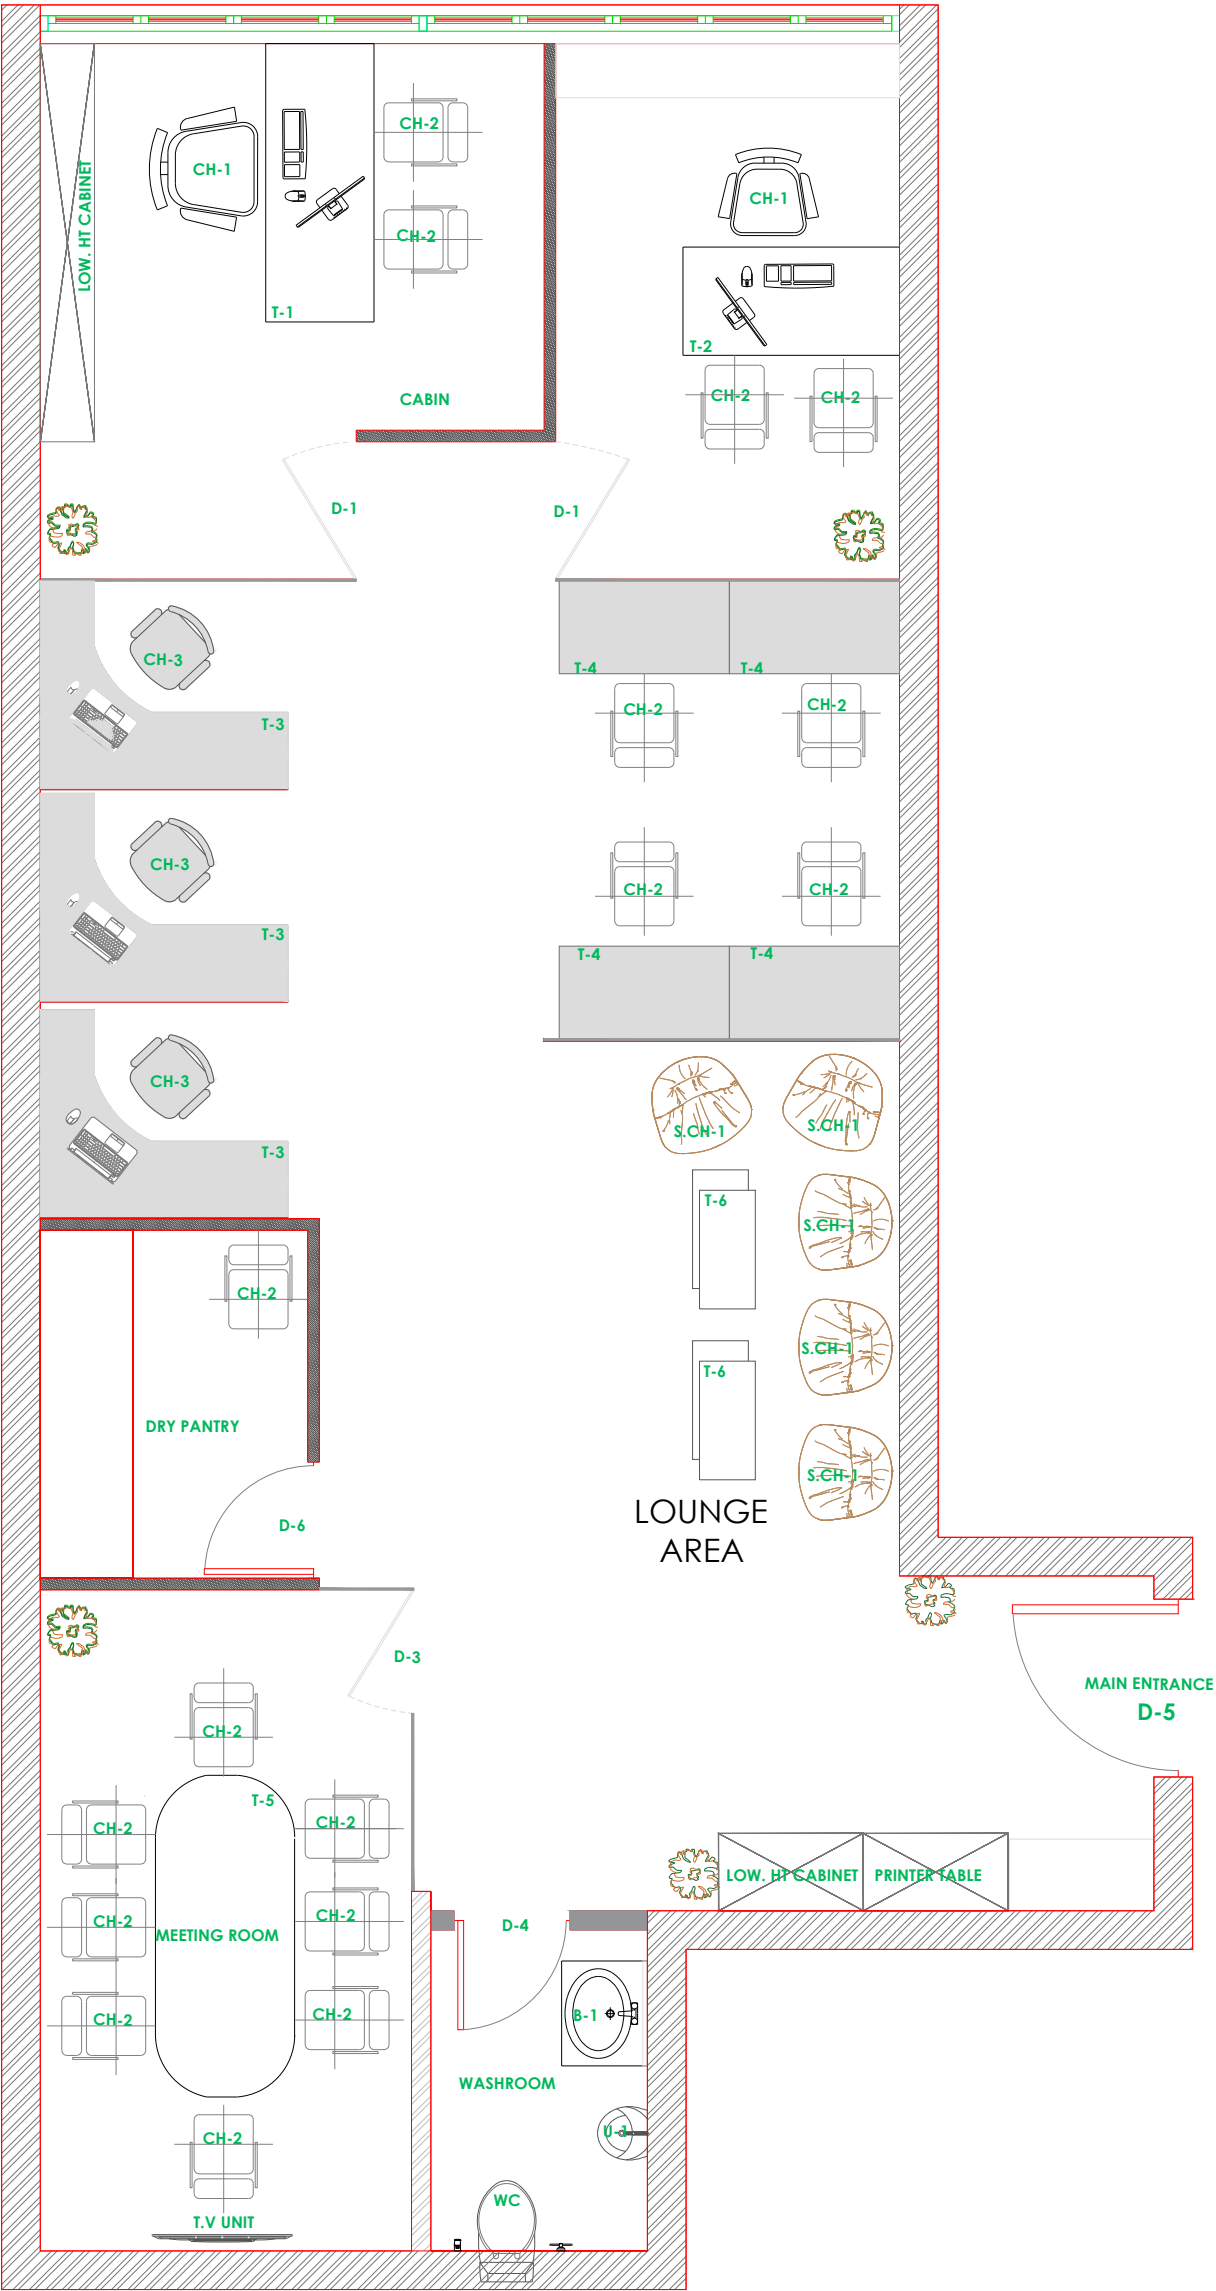

Note: All DIMENSIONS IN MM


Note: All dimensions to be checked on site

DRY PARTITION =

GLASS PARTITION =



PROJECT DETAILS		SITE DETAILS		DRAWING DETAILS			CLIENT	ARCHITECT
Project	RENOVATION WORK	Floor	-	Dwg Status	FURNITURE LAYOUT	03-03-2026		BIRD ENGINEERING PVT LTD.
Site	E-9 , 2RD FLOOR CP	Floor carpet Area	- 78.98 SQM	Dwg Title	INTERNAL LAYOUT	POOJA DAKSH		
Address	E-9, Connaught House, CP, New Delhi, 11001	B.O.Slab	-	Dwg No.	3	ABHISHEK DWIVEDI		
Channel P	-	B.O.Beam	-	Scale	Fit to paper			
		B.O.F.Ceiling	-	All the dimensions in millimeter				

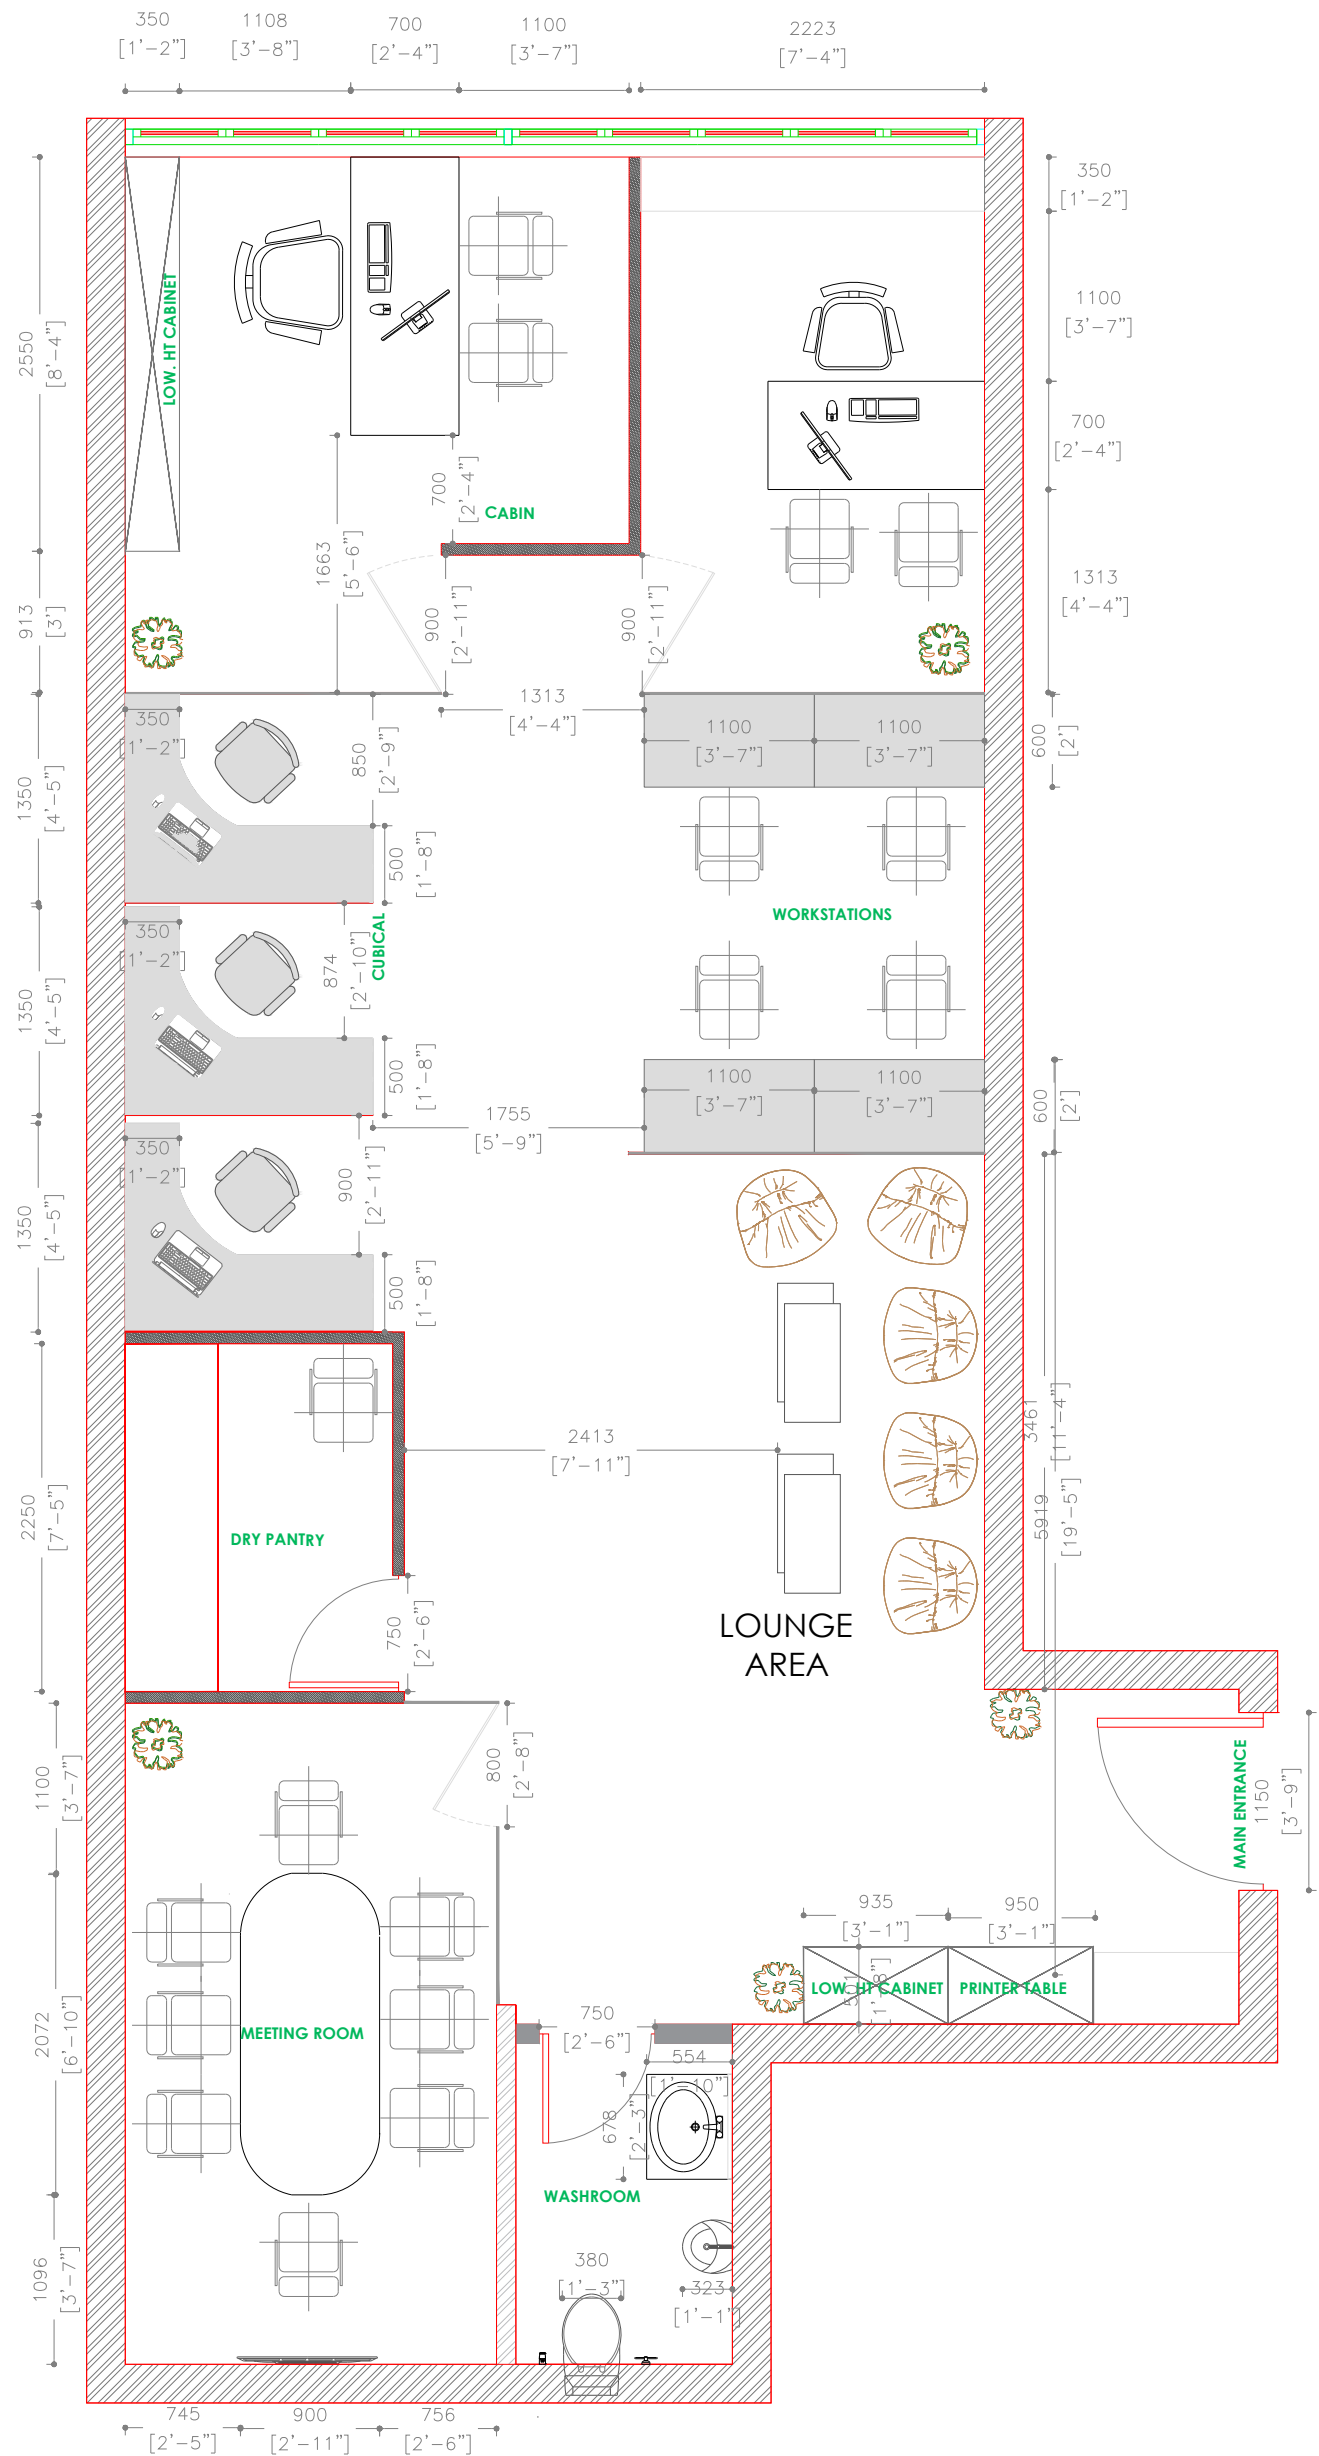

Note: All DIMENSIONS IN MM


Note: All dimensions to be checked on site

DRY PARTITION =

GLASS PARTITION =



PROJECT DETAILS		SITE DETAILS		DRAWING DETAILS			CLIENT	ARCHITECT
Project	RENOVATION WORK	Floor	-	Dwg Status	FURNITURE SETTING-OUT LAYOUT	03-03-2026		BIRD ENGINEERING PVT LTD.
Site	E-9 , 2RD FLOOR CP	Floor carpet Area	- 78.98 SQM	Dwg Title	INTERNAL LAYOUT	POOJA DAKSH		
Address	E-9, Connaught House, CP, New Delhi, 11001	B.O.Slab	-	Dwg No.	4	ABHISHEK DWIVEDI		
		B.O.Beam	-	Scale	Fit to paper			
Channel P	-	B.O.F.Ceiling	-	All the dimensions in millimeter				

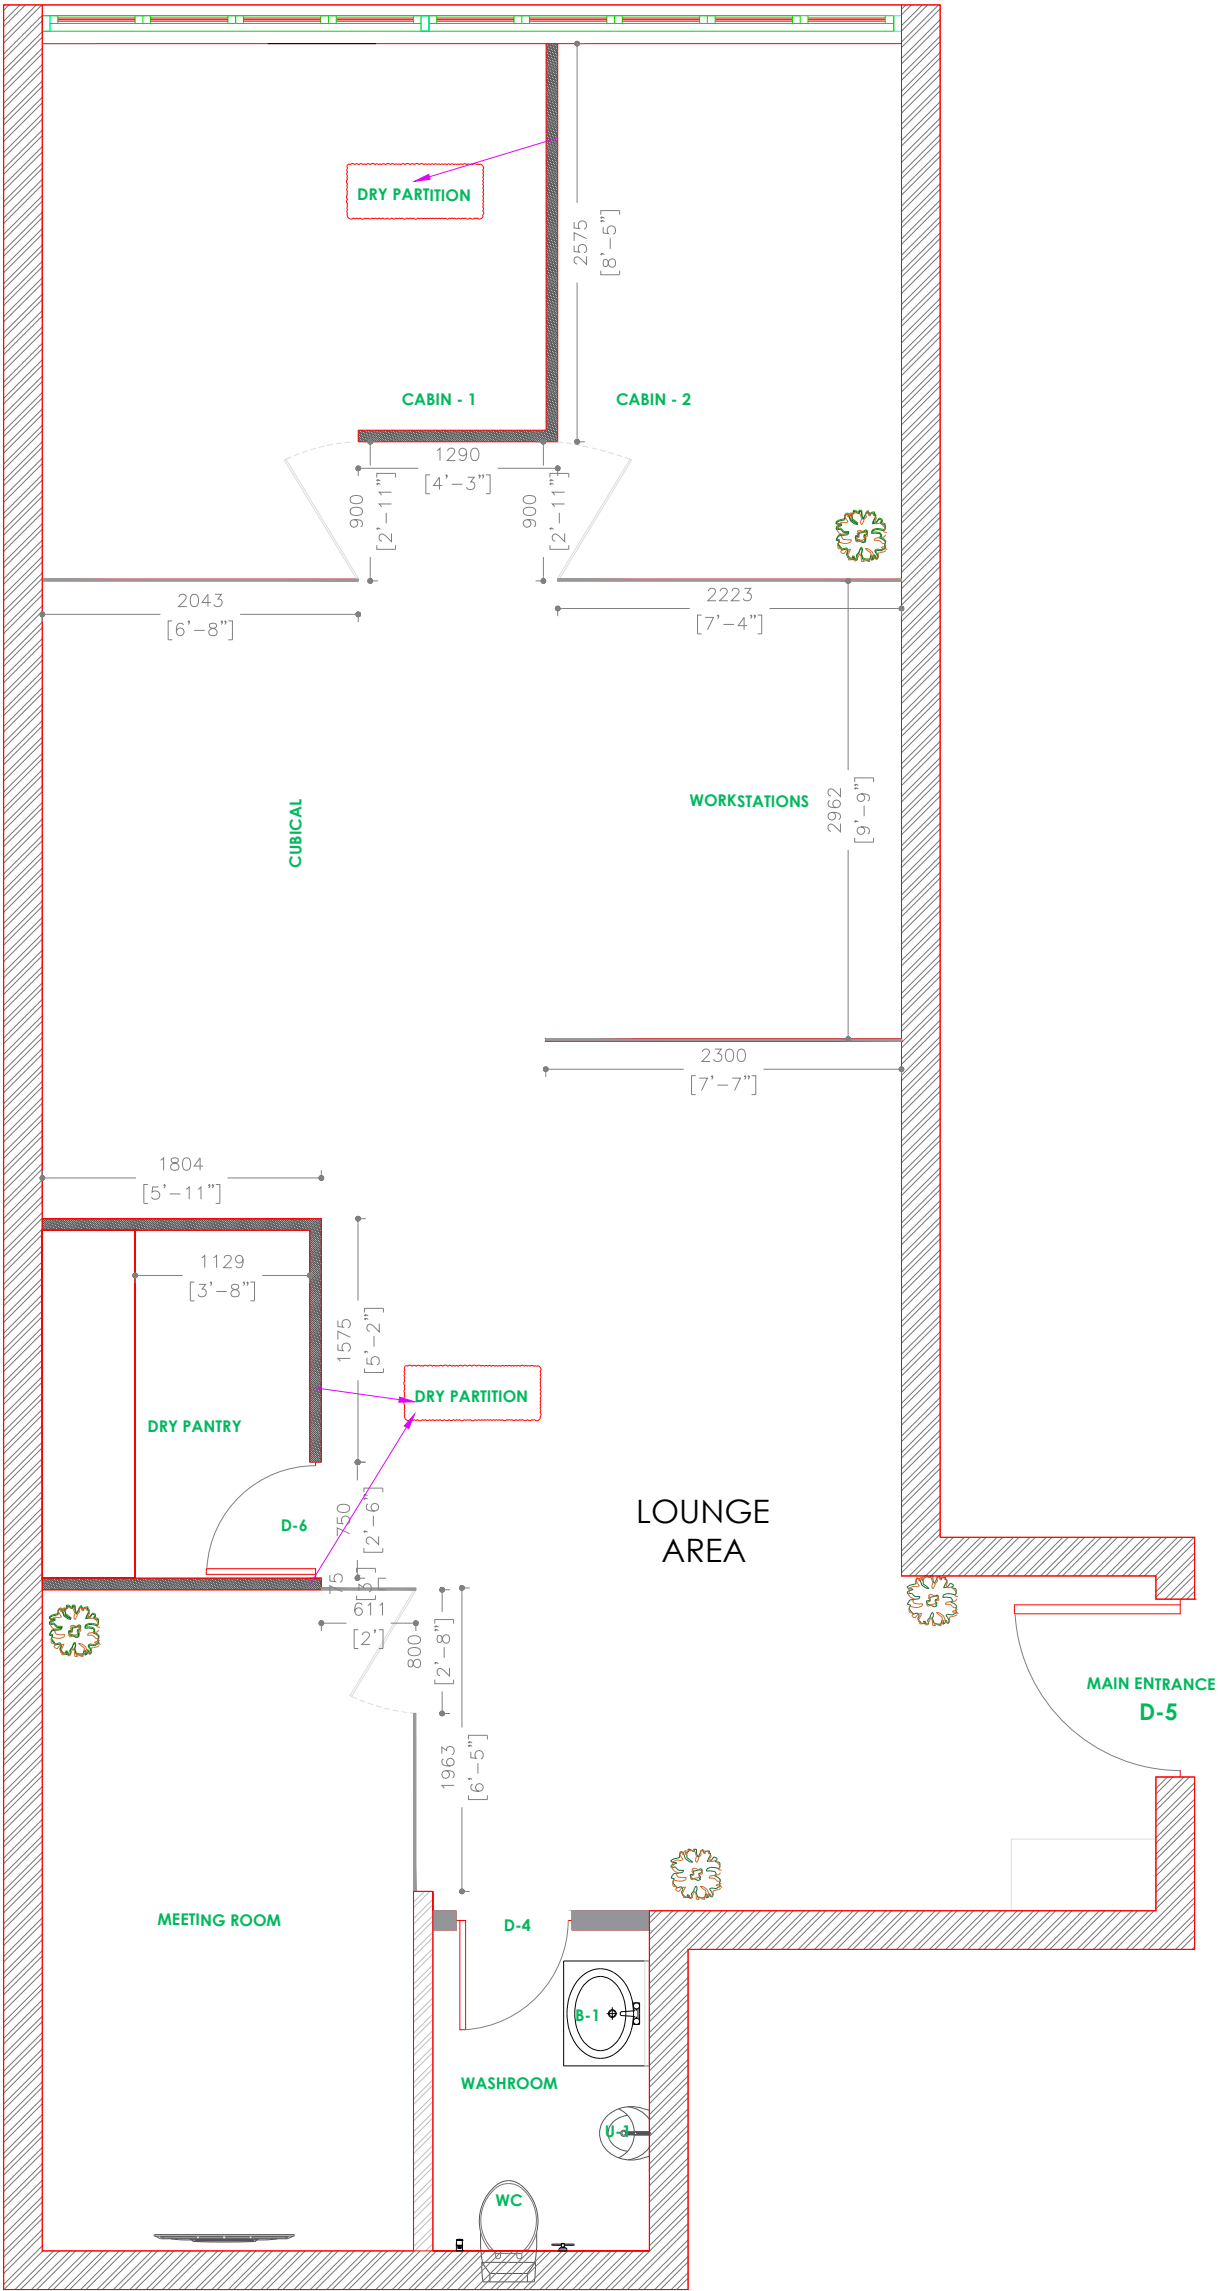


Note: All DIMENSIONS IN MM
Note: All dimensions to be checked on site

DRY PARTITION
GLASS PARTITION



PROJECT DETAILS		SITE DETAILS		DRAWING DETAILS			CLIENT	ARCHITECT
Project	RENOVATION WORK	Floor	-	Dwg Status	CIVIL GLAZING LAYOUT	03-03-2026		BIRD ENGINEERING PVT LTD.
Site	E-9 , 2RD FLOOR CP	Floor carpet Area	- 78.98 SQM	Dwg Title	INTERNAL LAYOUT	POOJA DAKSH		
Address	E-9, Connaught House, CP, New Delhi, 11001	B.O.Slab	-	Dwg No.	5	ABHISHEK DWIVEDI		
		B.O.Beam	-	Scale	Fit to paper			
Channel P	-	B.O.F.Ceiling	-	All the dimensions in millimeter				

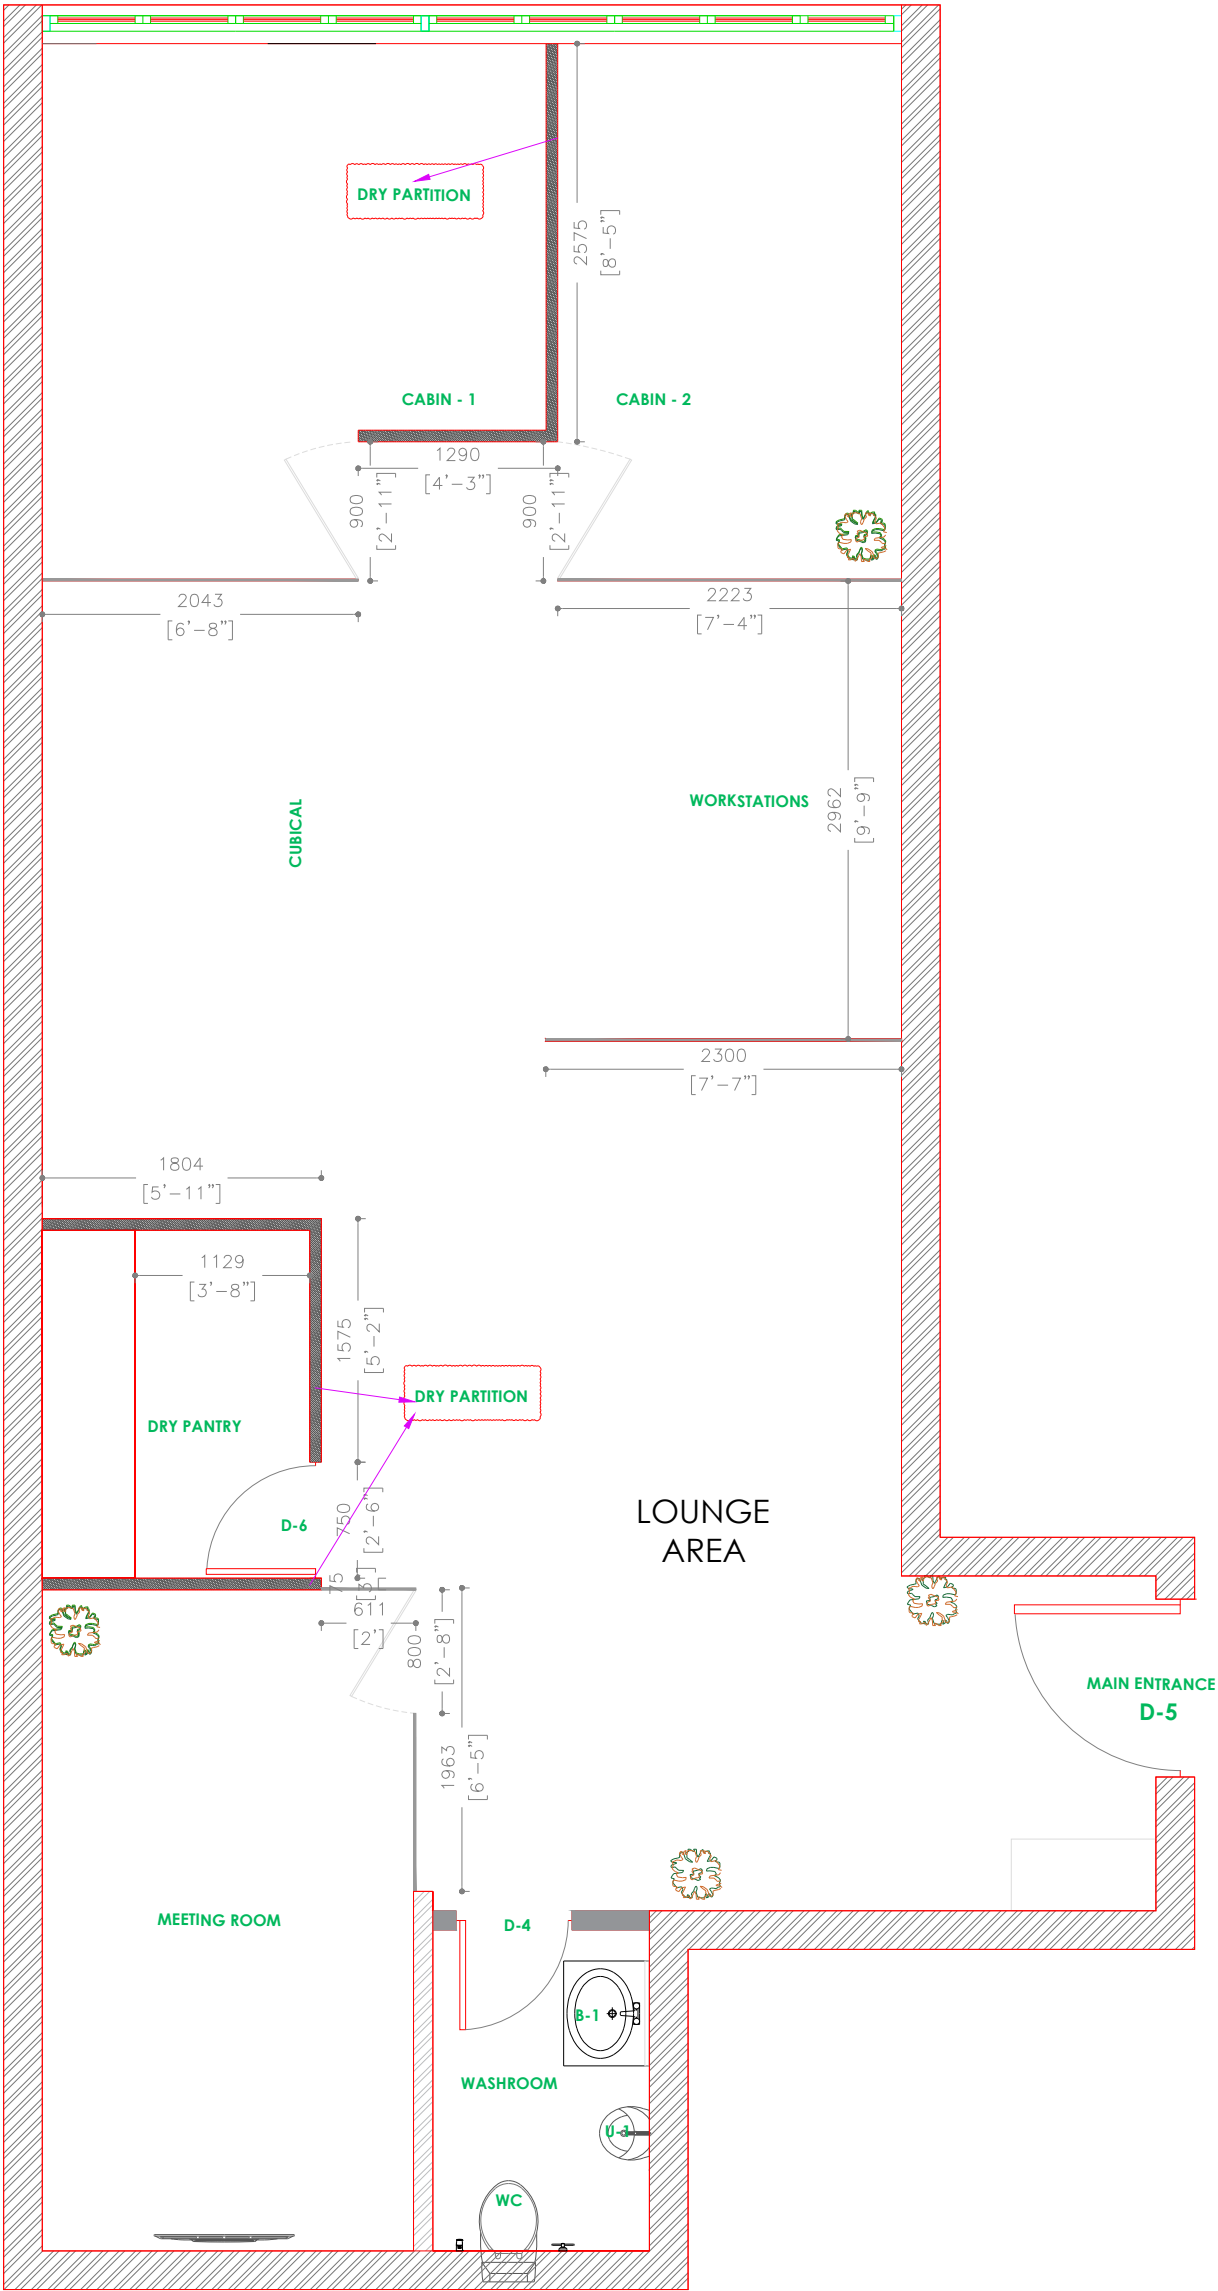


Note: All DIMENSIONS IN MM
Note: All dimensions to be checked on site

DRY PARTITION
GLASS PARTITION




PROJECT DETAILS		SITE DETAILS		DRAWING DETAILS			CLIENT	ARCHITECT
Project	RENOVATION WORK	Floor	-	Dwg Status	CIVIL GLAZING LAYOUT	03-03-2026		BIRD ENGINEERING PVT LTD.
Site	E-9 , 2RD FLOOR CP	Floor carpet Area	- 78.98 SQM	Dwg Title	INTERNAL LAYOUT	POOJA DAKSH		
Address	E-9, Connaught House, CP, New Delhi, 11001	B.O.Slab	-	Dwg No.	5	ABHISHEK DWIVEDI		
		B.O.Beam	-	Scale	Fit to paper			
Channel P	-	B.O.F.Ceiling	-	All the dimensions in millimeter				

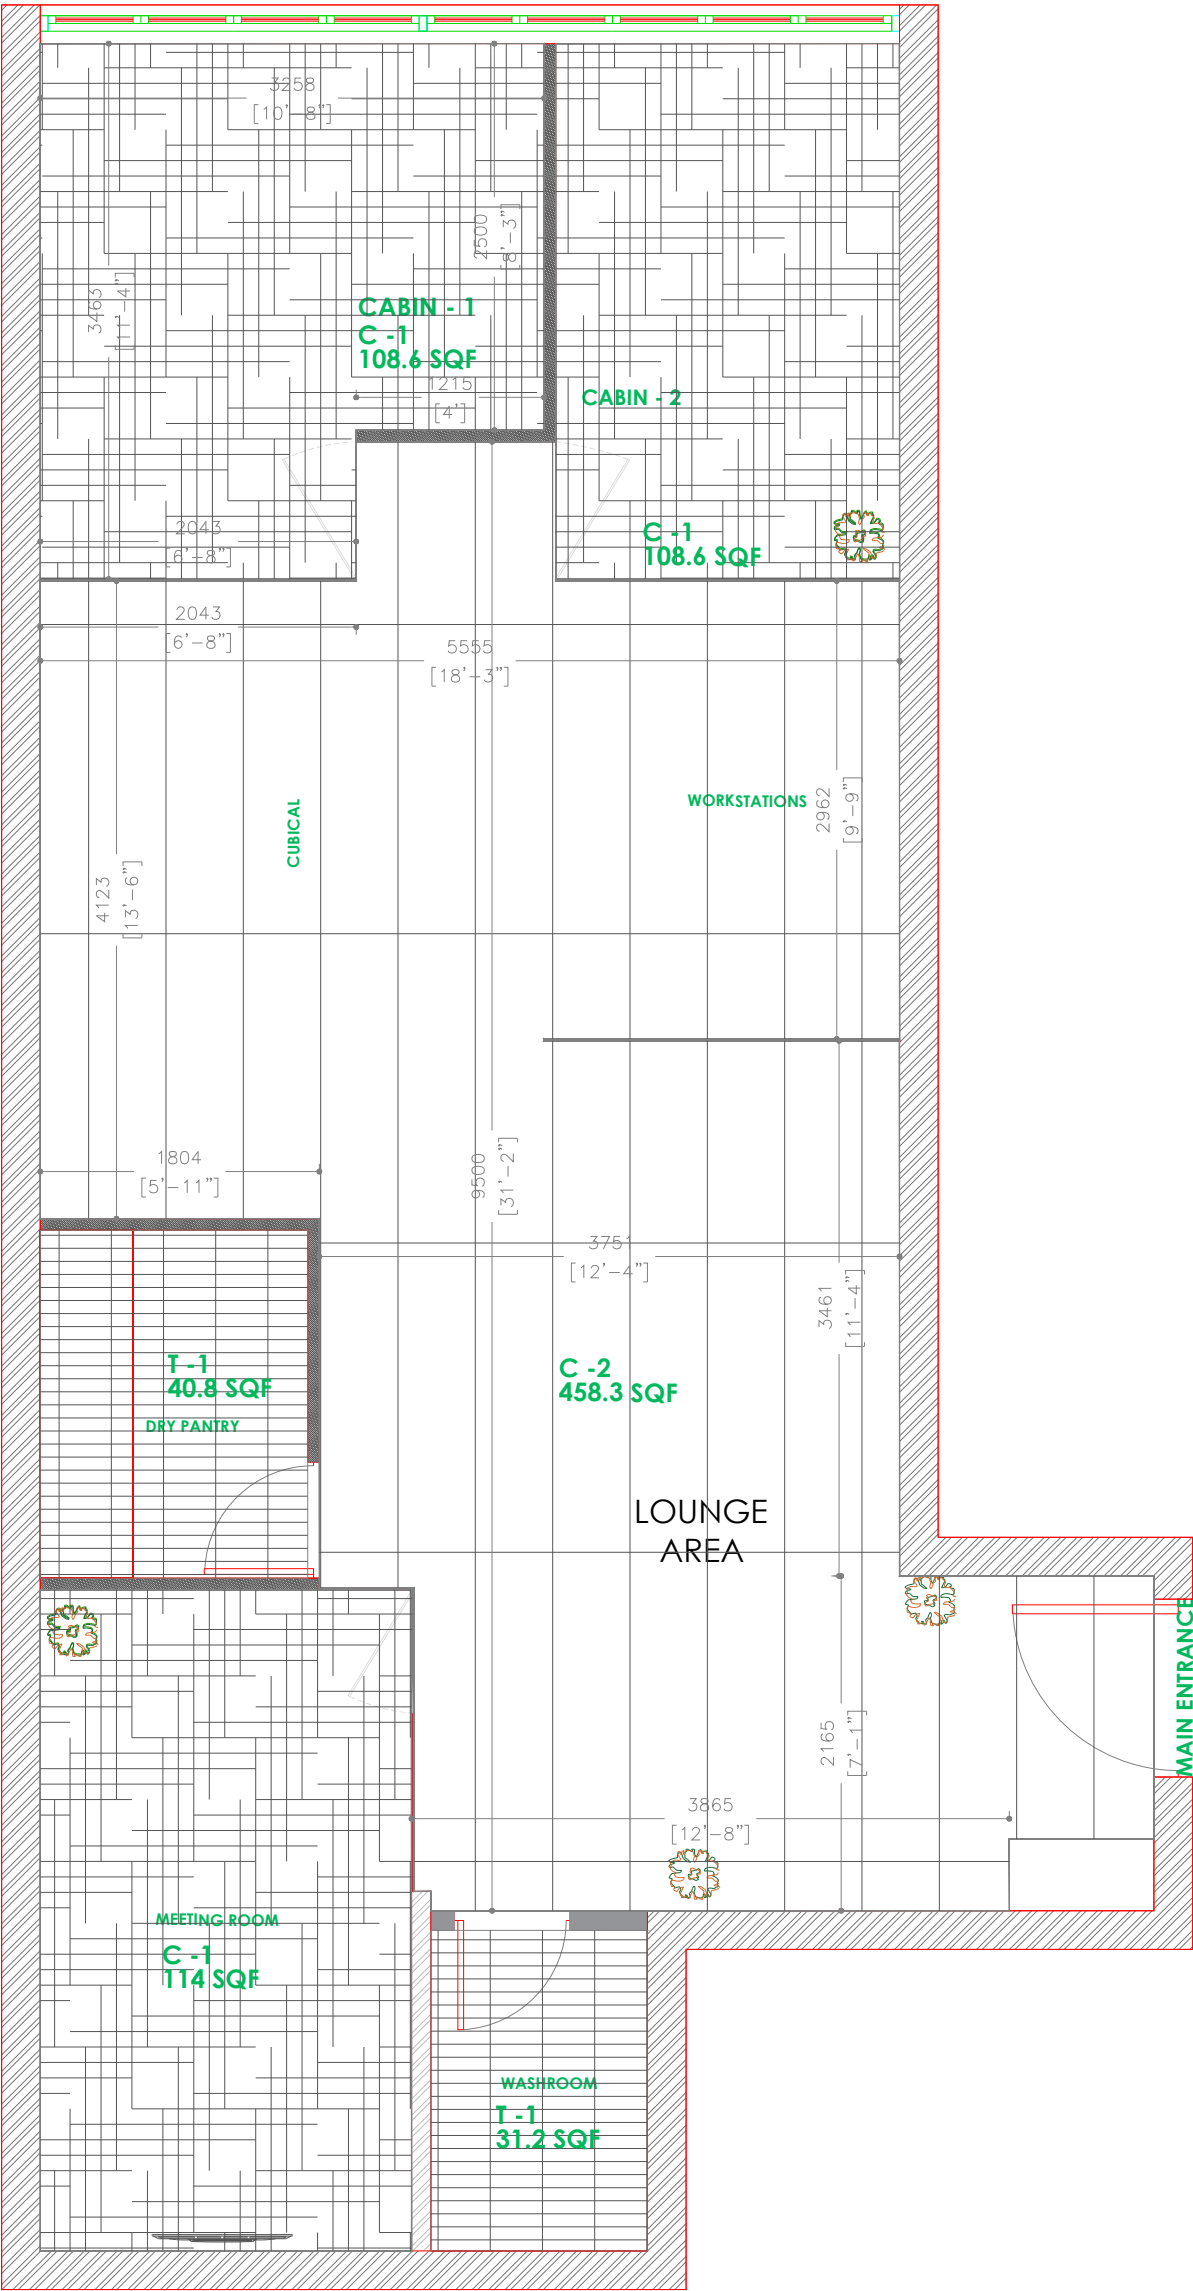


Note: All DIMENSIONS IN MM

Note: All dimensions to be checked on site

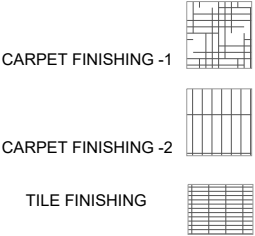

PROJECT DETAILS		SITE DETAILS		DRAWING DETAILS			CLIENT	ARCHITECT
Project	RENOVATION WORK	Floor	-	Dwg Status	FLOORING LAYOUT	03-03-2026		BIRD ENGINEERING PVT LTD.
Site	E-9 , 2RD FLOOR CP	Floor carpet Area	- 78.98 SQM	Dwg Title	INTERNAL LAYOUT	POOJA DAKSH		
Address	E-9, Connaught House, CP, New Delhi, 11001	B.O.Slab	-	Dwg No.	6	ABHISHEK DWIVEDI		
		B.O.Beam	-	Scale	Fit to paper			
Channel P	-	B.O.F.Ceiling	-	All the dimensions in millimeter				

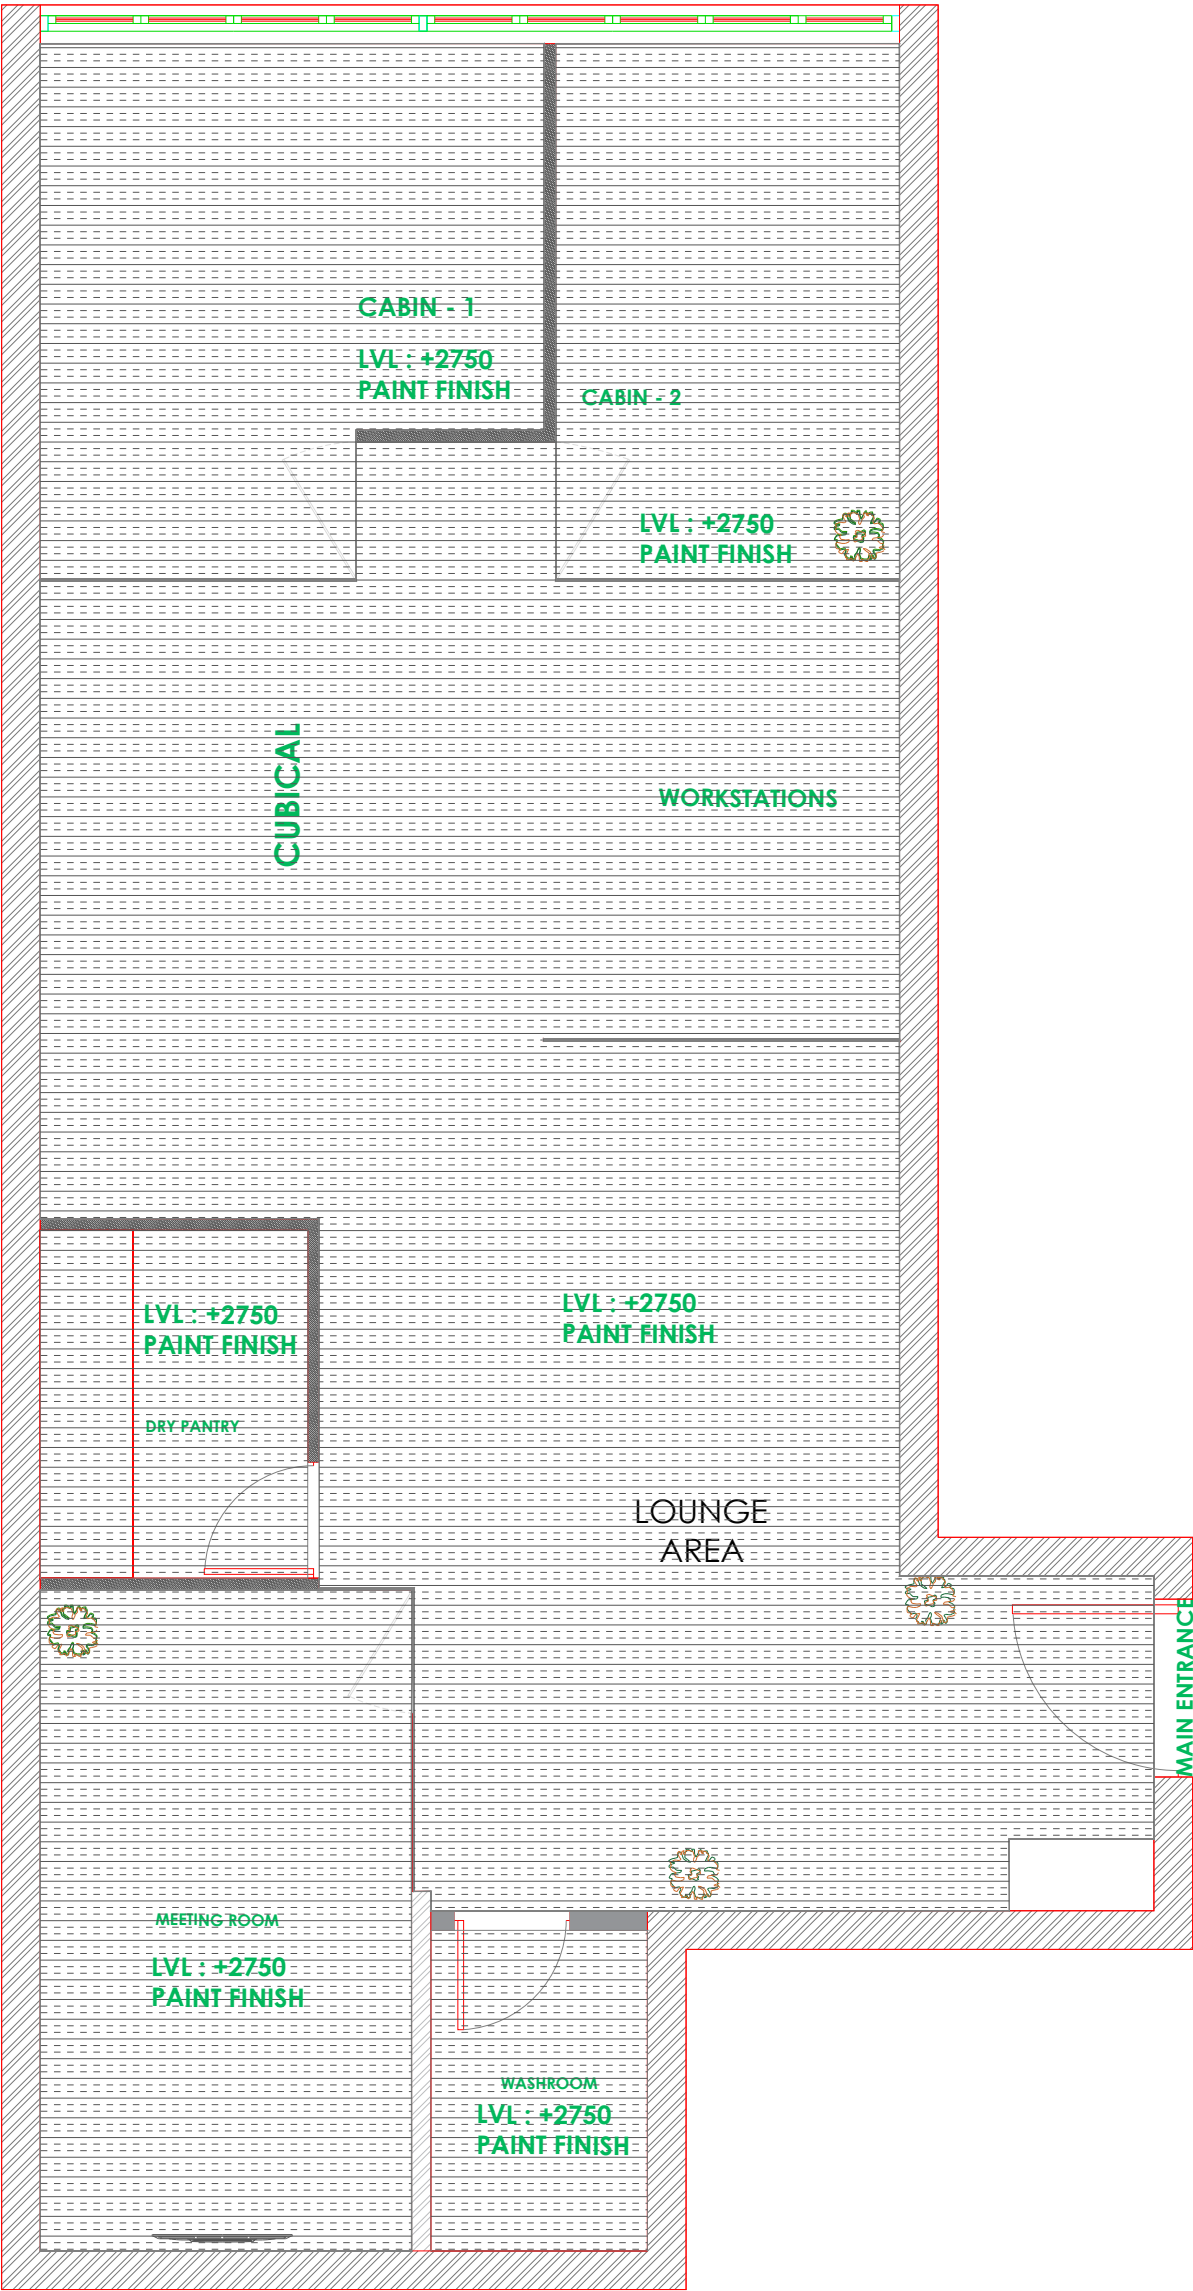

Note: All DIMENSIONS IN MM

Note: All dimensions to be checked on site



PROJECT DETAILS		SITE DETAILS		DRAWING DETAILS			CLIENT	ARCHITECT
Project	RENOVATION WORK	Floor	-	Dwg Status	CEILING LAYOUT	03-03-2026		BIRD ENGINEERING PVT LTD.
Site	E-9 , 2RD FLOOR CP	Floor carpet Area	- 78.98 SQM	Dwg Title	INTERNAL LAYOUT	POOJA DAKSH		
Address	E-9, Connaught House, CP, New Delhi, 11001	B.O.Slab	-	Dwg No.	7	ABHISHEK DWIVEDI		
		B.O.Beam	-	Scale	Fit to paper			
Channel P	-	B.O.F.Ceiling	-	All the dimensions in millimeter				