


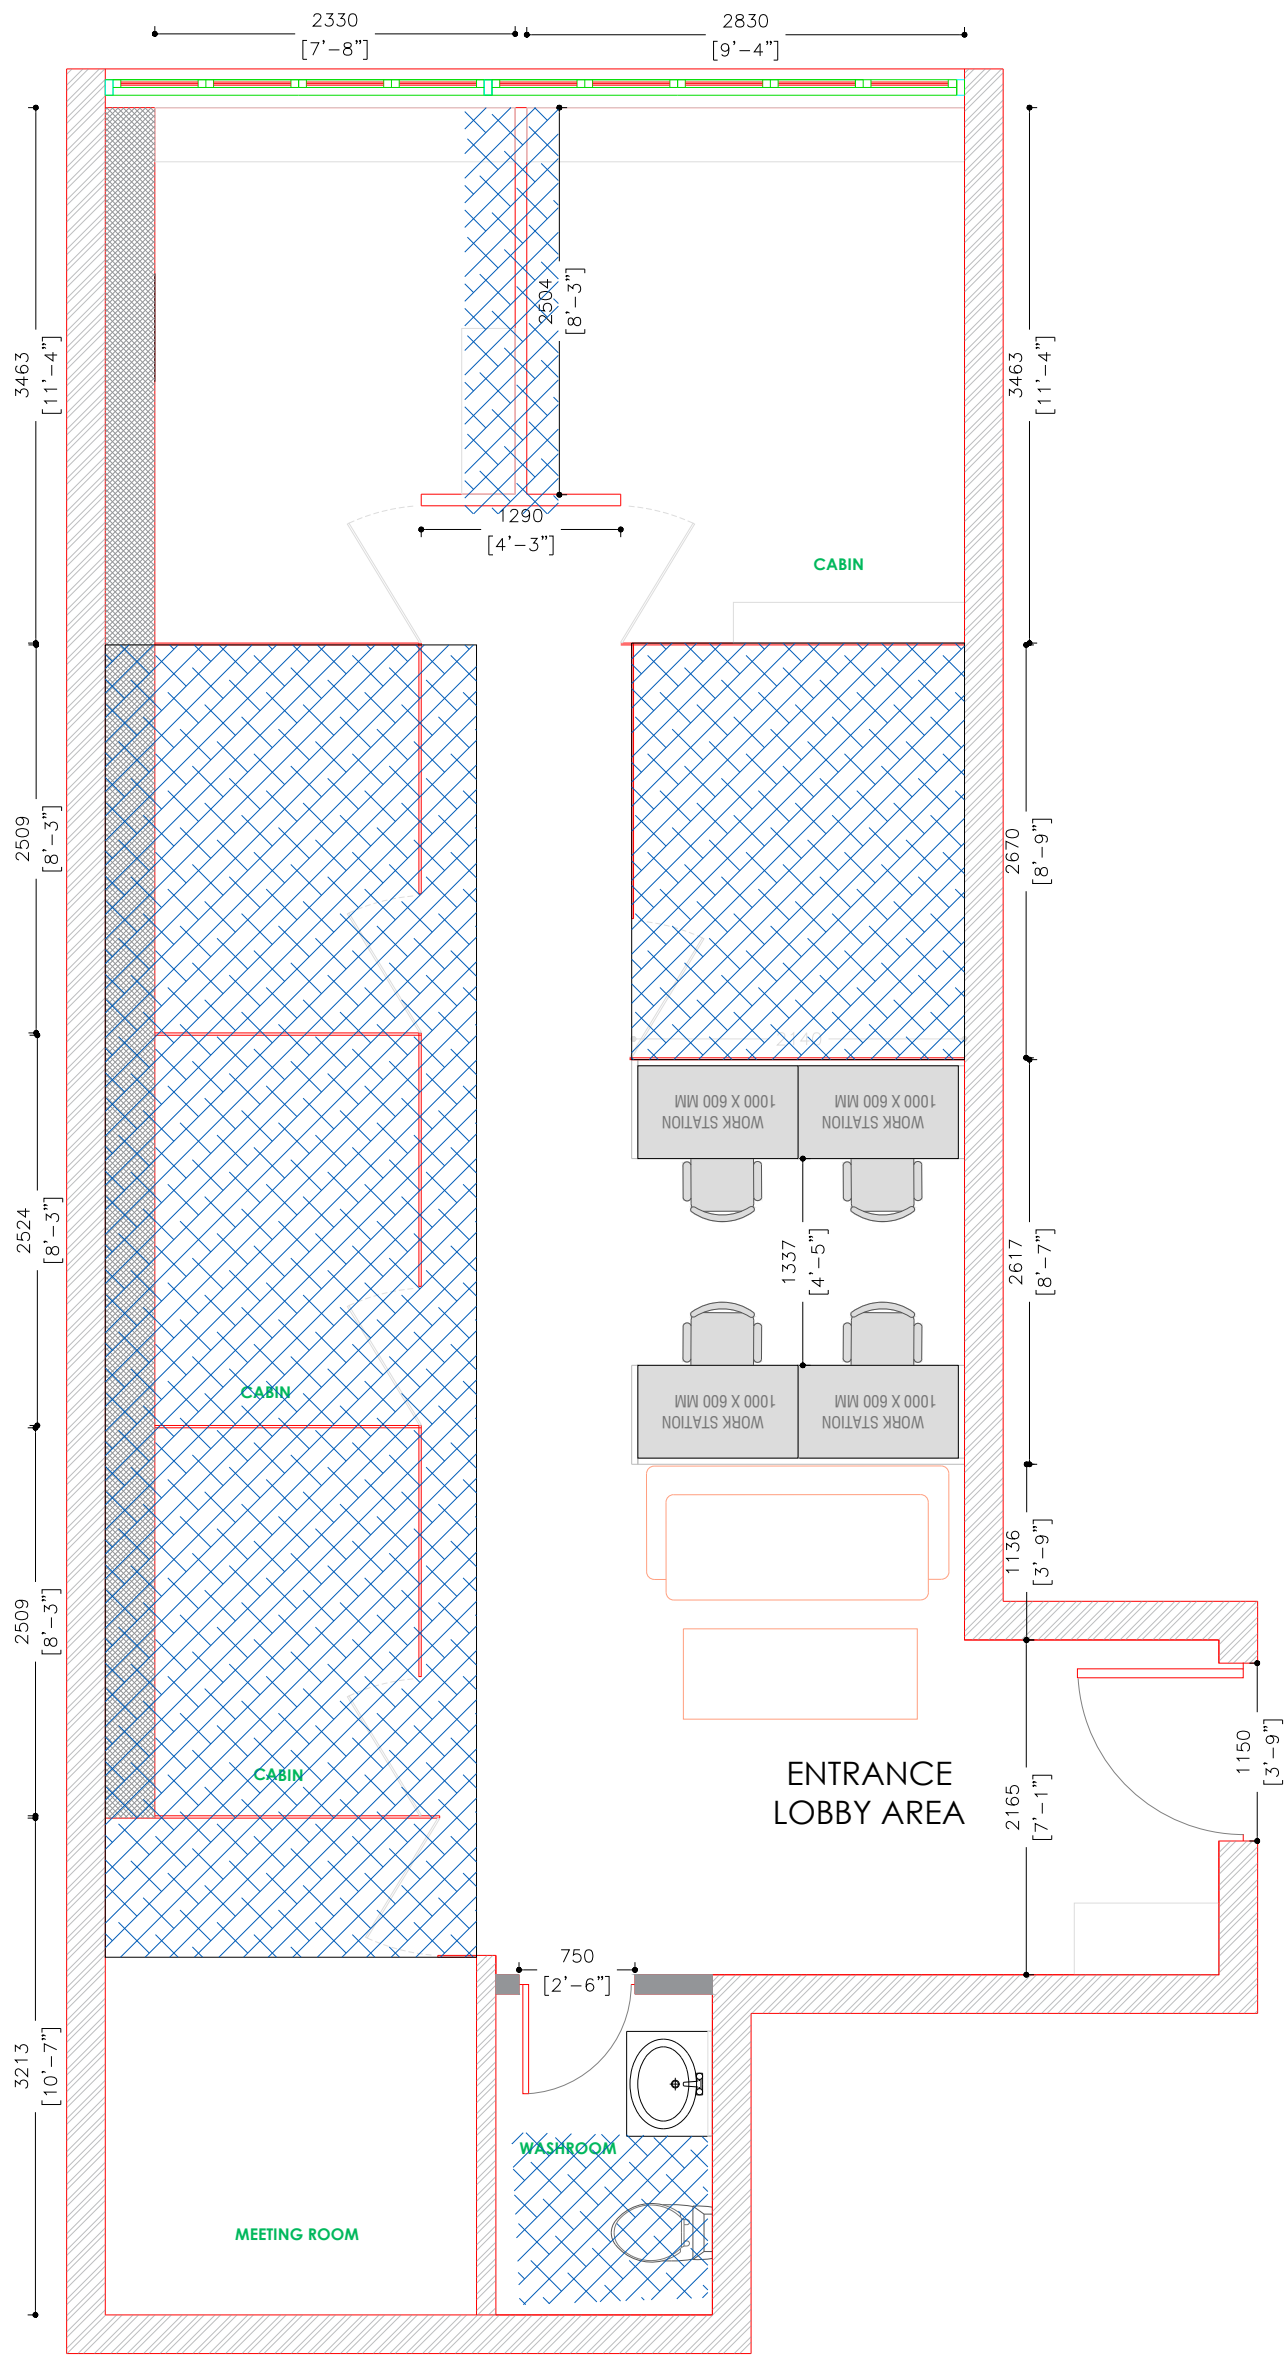

Note: All DIMENSIONS IN MM

Note: All dimensions to be checked on site



PROJECT DETAILS		SITE DETAILS		DRAWING DETAILS				CLIENT	ARCHITECT
Project	RENOVATION WORK	Floor	-	Dwg Status	DISMANTLING LAYOUT		Date	03-03-2026	BIRD ENGINEERING PVT LTD.
Site	E-9 , 2RD FLOOR CP	Floor carpet Area	- 78.98 SQM	Dwg Title	INTERNAL LAYOUT		Dwn by	POOJA DAKSH	
Address	E-9, Connaught House, CP, New Delhi, 11001	B.O.Slab	-	Dwg No.	2		Chk By	ABHISHEK DWIVEDI	
Channel P	-	B.O.Beam	-	Scale	Fit to paper				
		B.O.F.Ceiling	-	All the dimensions in millimeter					