


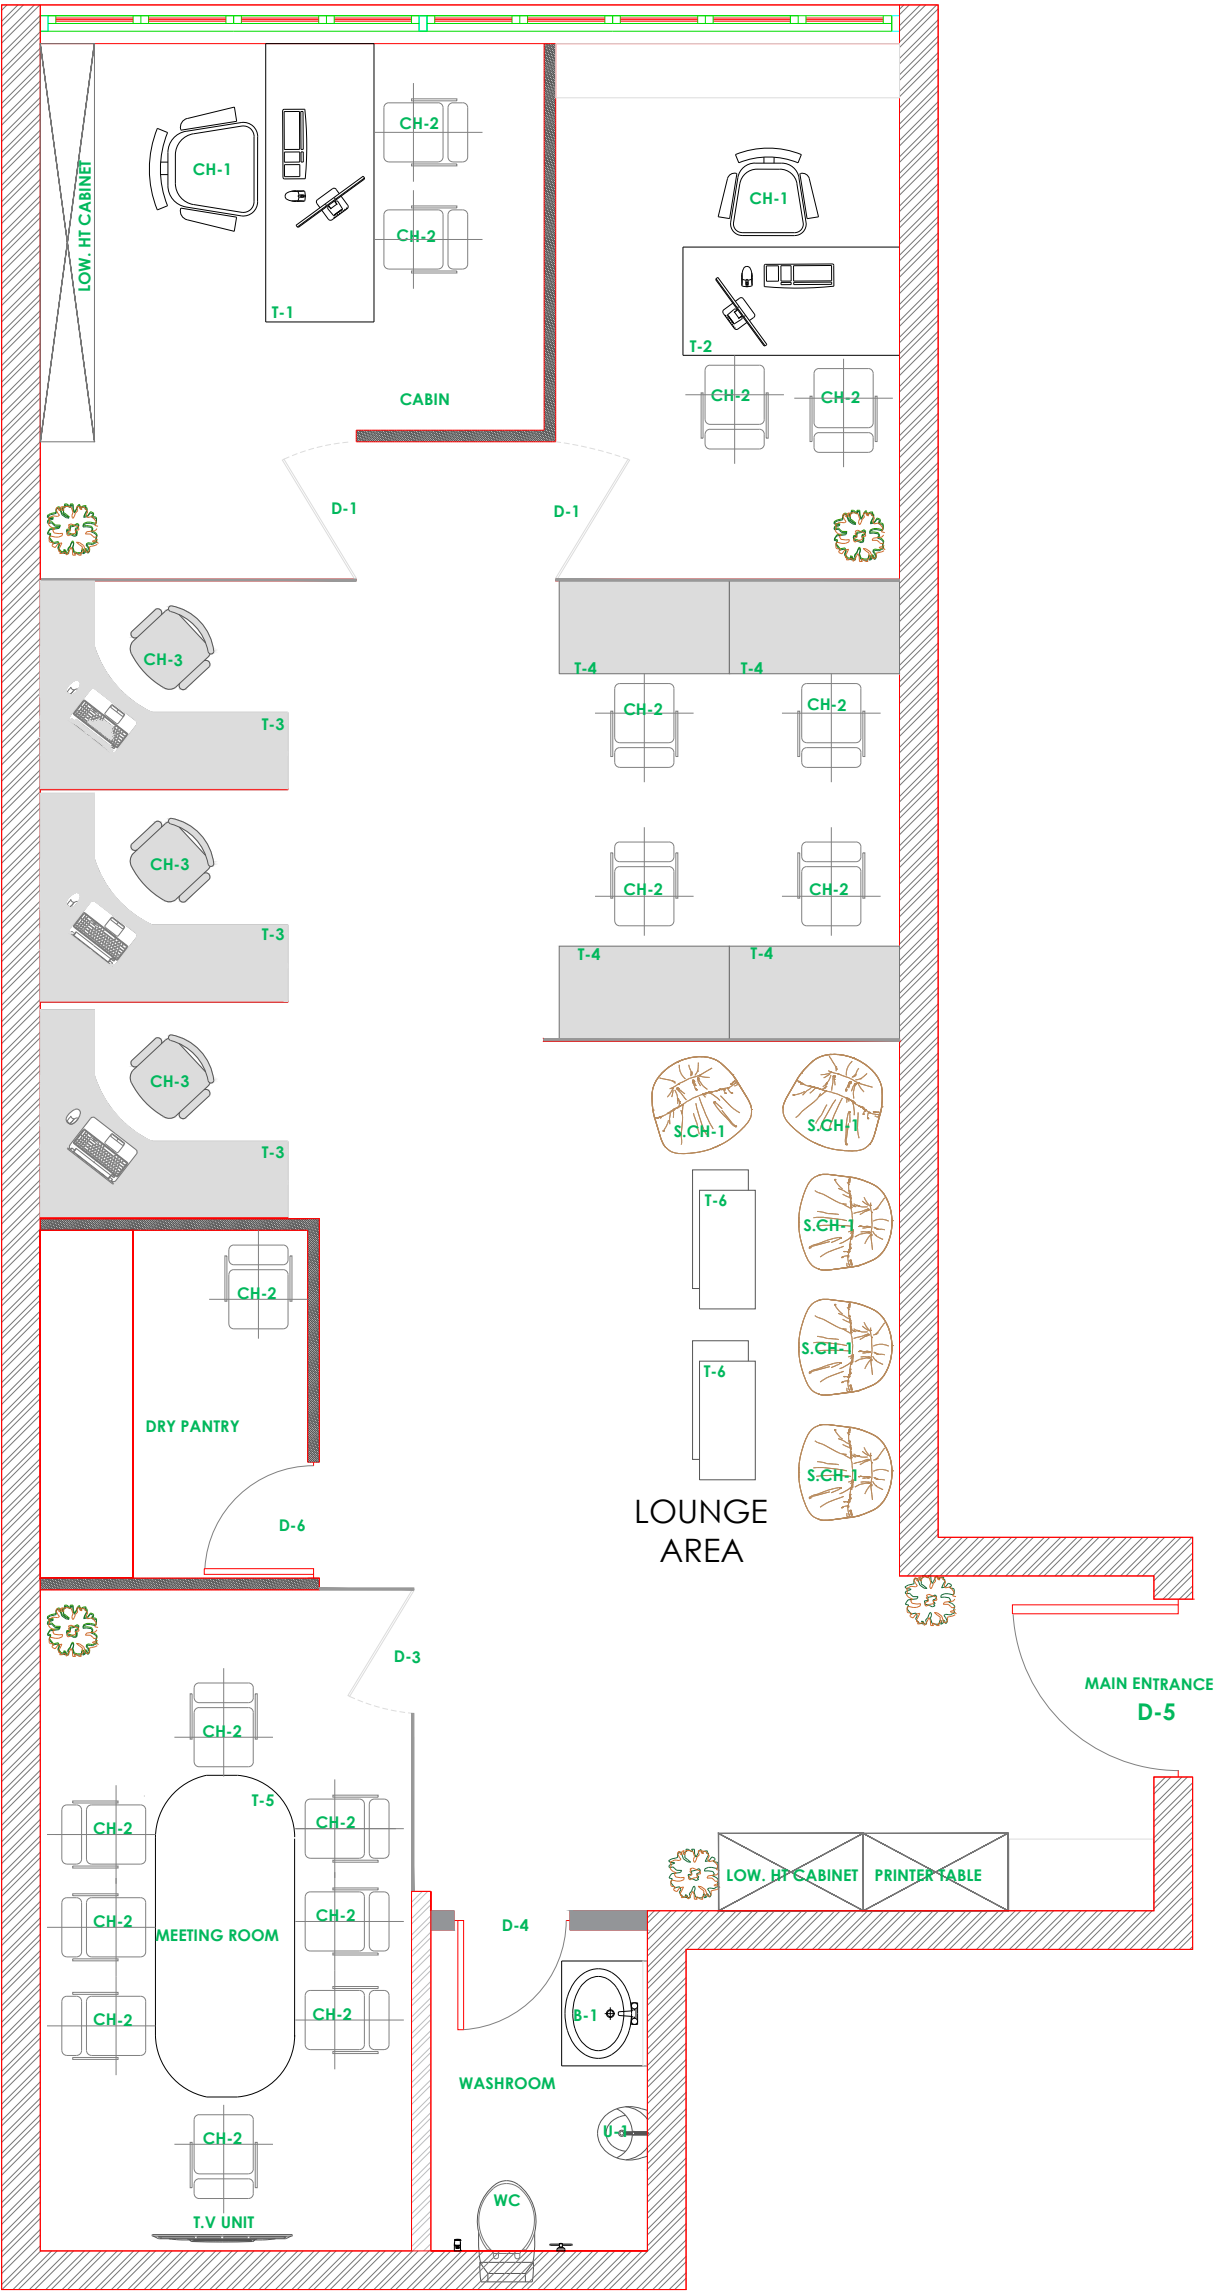

Note: All DIMENSIONS IN MM

Note: All dimensions to be checked on site

DRY PARTITION =

GLASS PARTITION =



PROJECT DETAILS		SITE DETAILS		DRAWING DETAILS			CLIENT	ARCHITECT
Project	RENOVATION WORK	Floor	-	Dwg Status	FURNITURE LAYOUT	03-03-2026		BIRD ENGINEERING PVT LTD.
Site	E-9 , 2RD FLOOR CP	Floor carpet Area	- 78.98 SQM	Dwg Title	INTERNAL LAYOUT	POOJA DAKSH		
Address	E-9, Connaught House, CP, New Delhi, 11001	B.O.Slab	-	Dwg No.	3	ABHISHEK DWIVEDI		
		B.O.Beam	-	Scale	Fit to paper			
Channel P	-	B.O.F.Ceiling	-	All the dimensions in millimeter				