


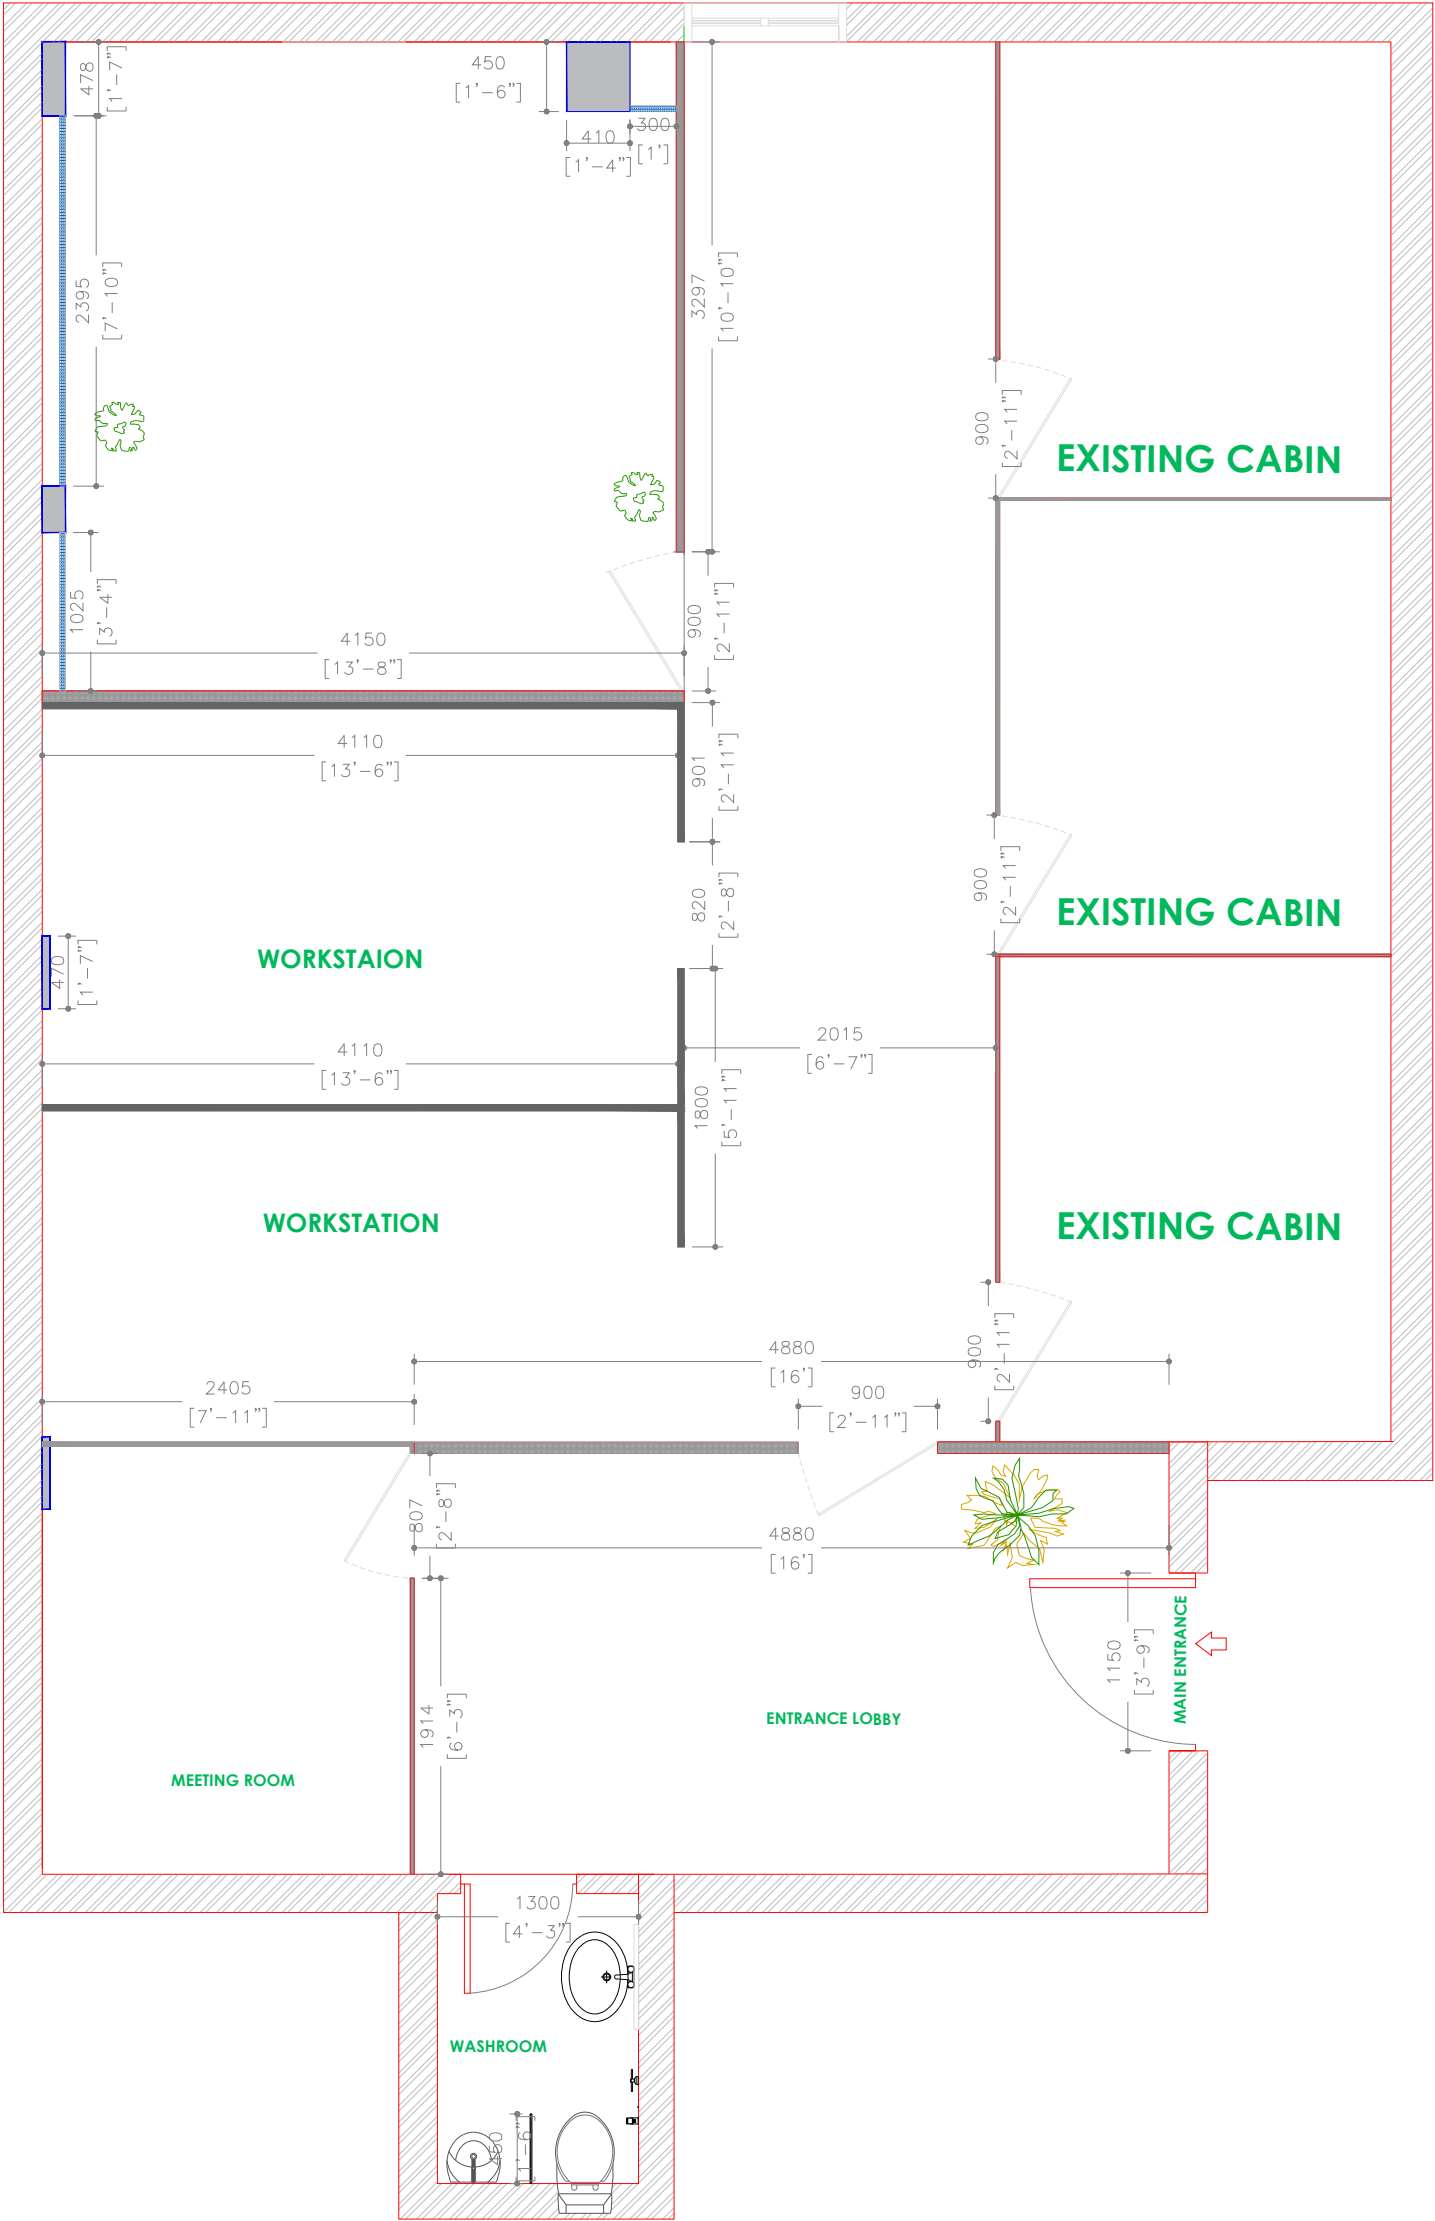

Note: All DIMENSIONS IN MM

Note: All dimensions to be checked on site

DRY PARTITION
GLASS PARTITION
WOOD PANNEL

PROJECT DETAILS		SITE DETAILS		DRAWING DETAILS				CLIENT	ARCHITECT
Project	RENOVATION WORK	Floor	-	Dwg Status	CIVIL GLAZING LAYOUT	Date	03-03-2026		BIRD ENGINEERING PVT LTD.
Site	E-9 , 3RD FLOOR CP	Floor carpet Area	- 101.90 SQM	Dwg Title	INTERNAL LAYOUT	Dwn by	POOJA DAKSH		
Address	E-9, Connaught House, CP, New Delhi, 11001	B.O.Slab	-	Dwg No.	5	Chk By	ABHISHEK DWIVEDI		
Channel P	-	B.O.Beam	-	Scale	Fit to paper				
		B.O.F.Ceiling	-	All the dimensions in millimeter					