


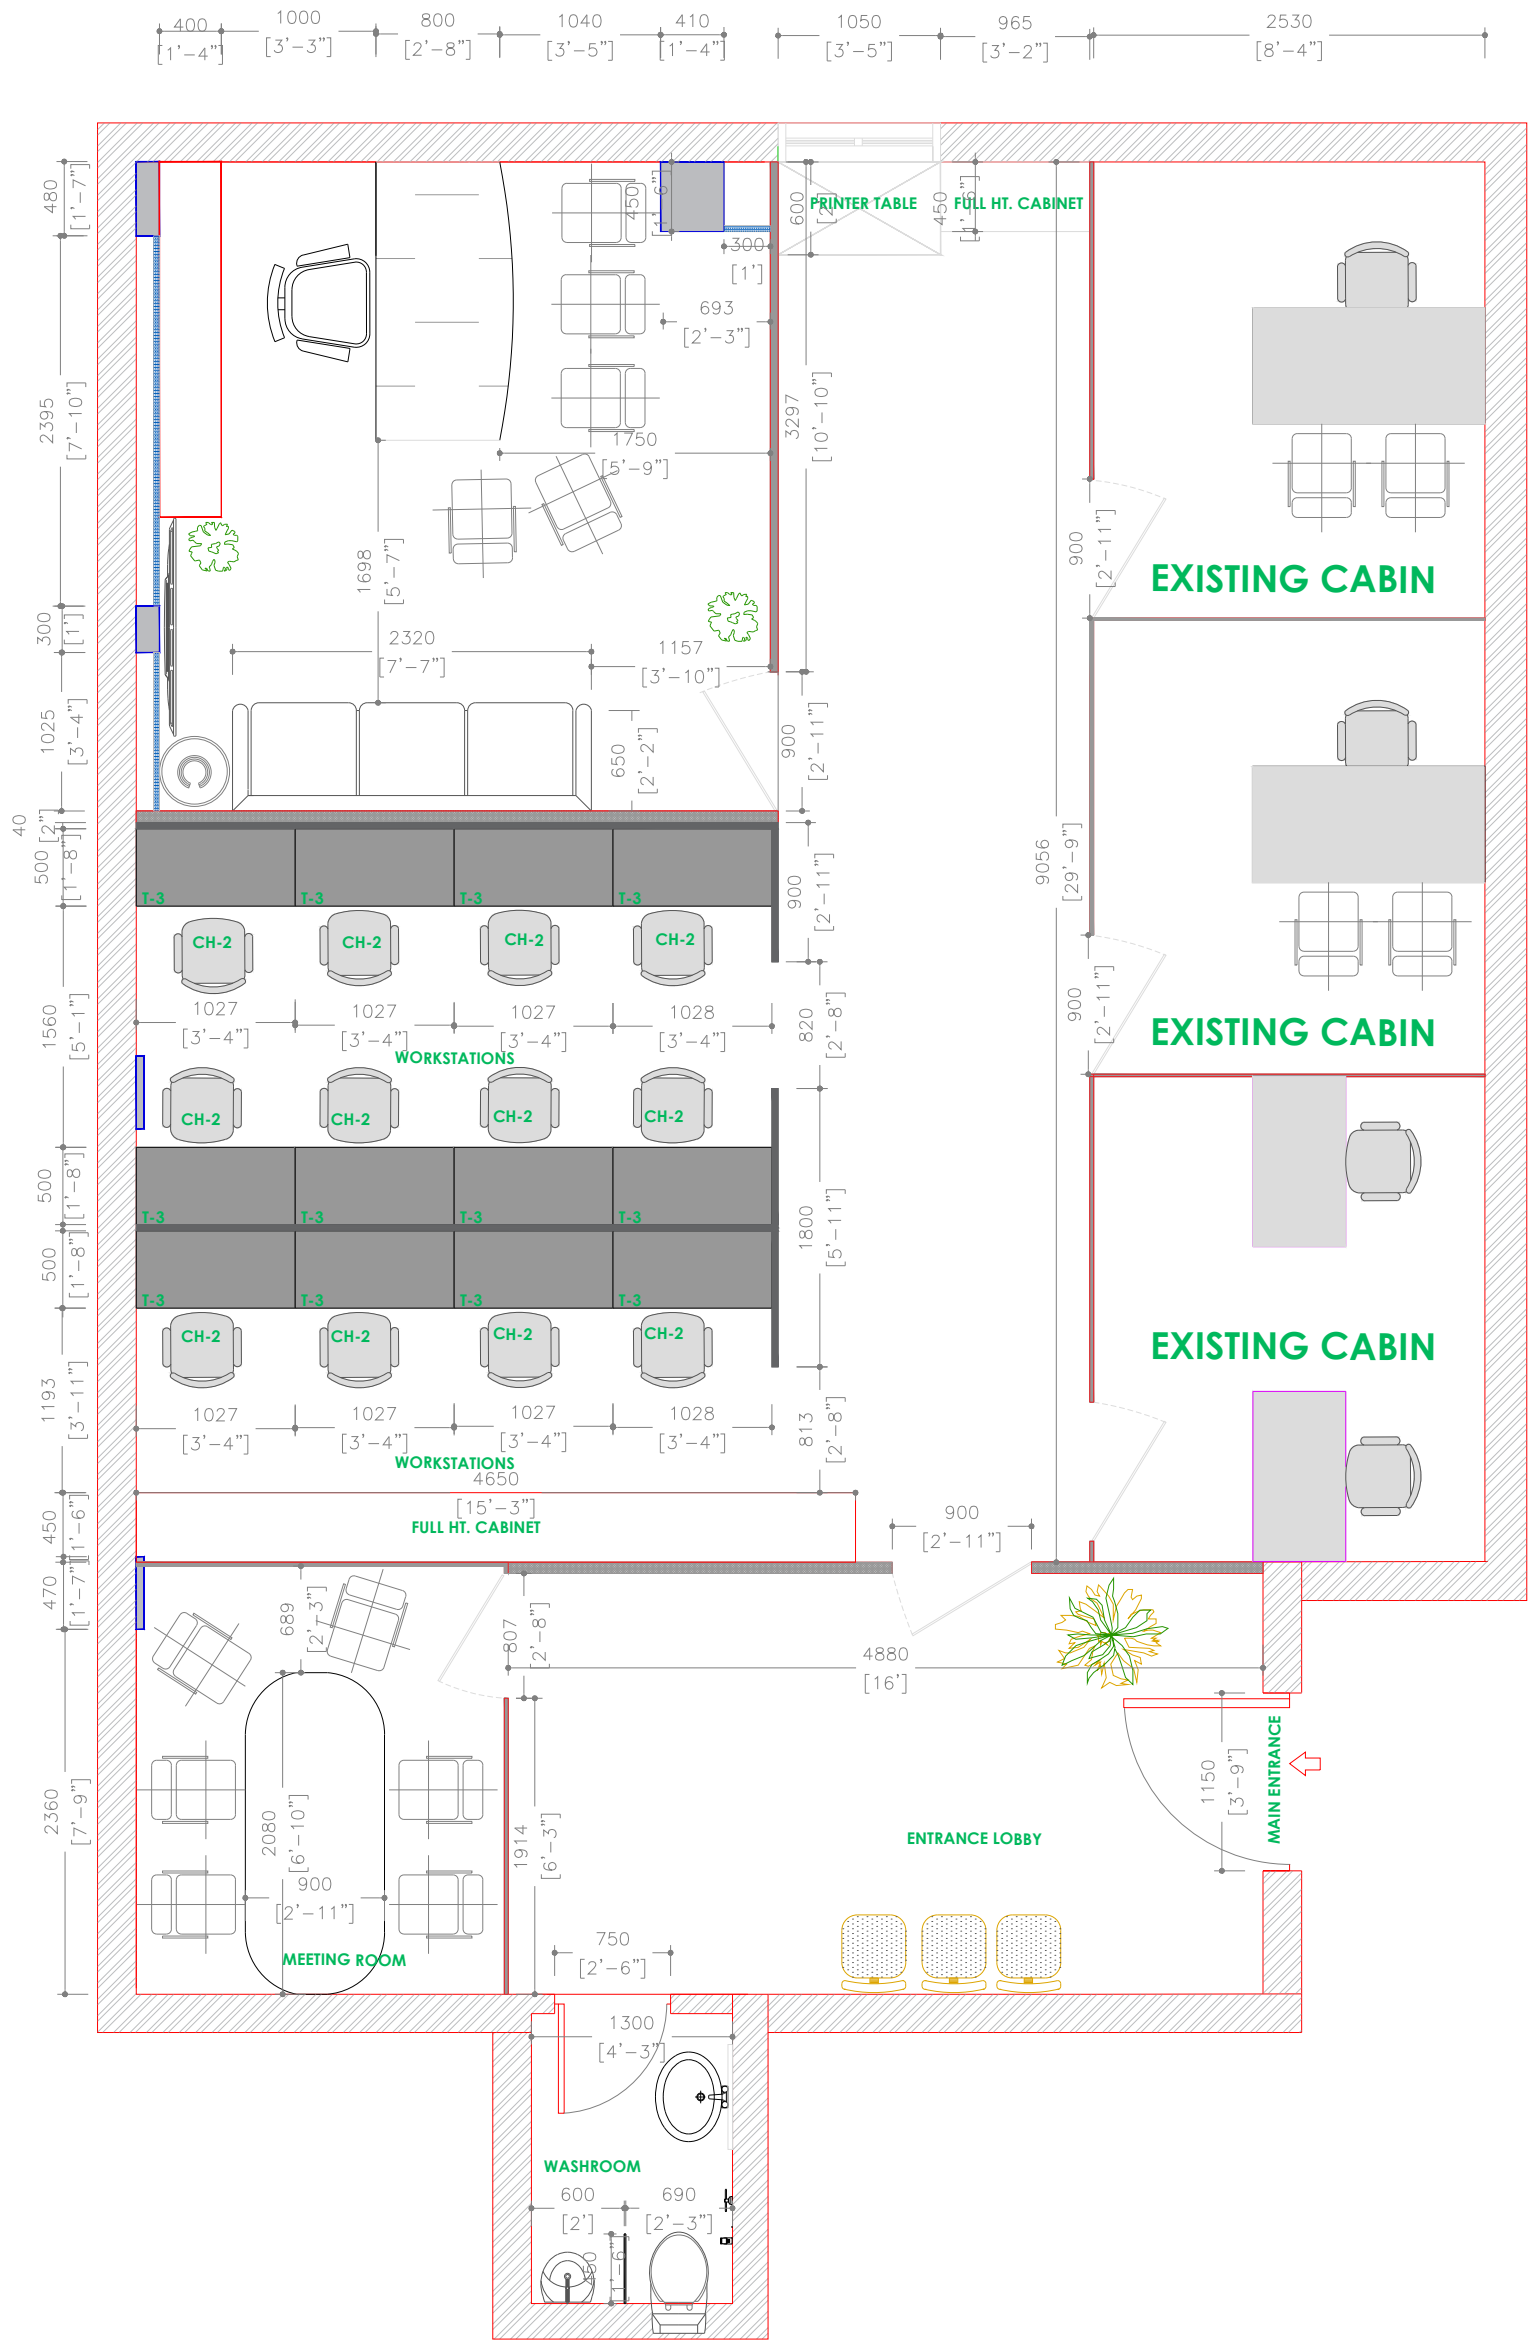

Note: All DIMENSIONS IN MM
Note: All dimensions to be checked on site

PROJECT DETAILS		SITE DETAILS		DRAWING DETAILS			CLIENT	ARCHITECT
Project	RENOVATION WORK	Floor	-	Dwg Status	FURNITURE SETTING-OUT LAYOUT	Date	03-03-2026	BIRD ENGINEERING PVT LTD.
Site	E-9 , 3RD FLOOR CP	Floor carpet Area	- 101.90 SQM	Dwg Title	INTERNAL LAYOUT	Dwn by	POOJA DAKSH	
Address	E-9, Connaught House, CP, New Delhi, 11001	B.O.Slab	-	Dwg No.	4	Chk By	ABHISHEK DWIVEDI	
Channel P	-	B.O.Beam	-	Scale	Fit to paper			
		B.O.F.Ceiling	-	All the dimensions in millimeter				