


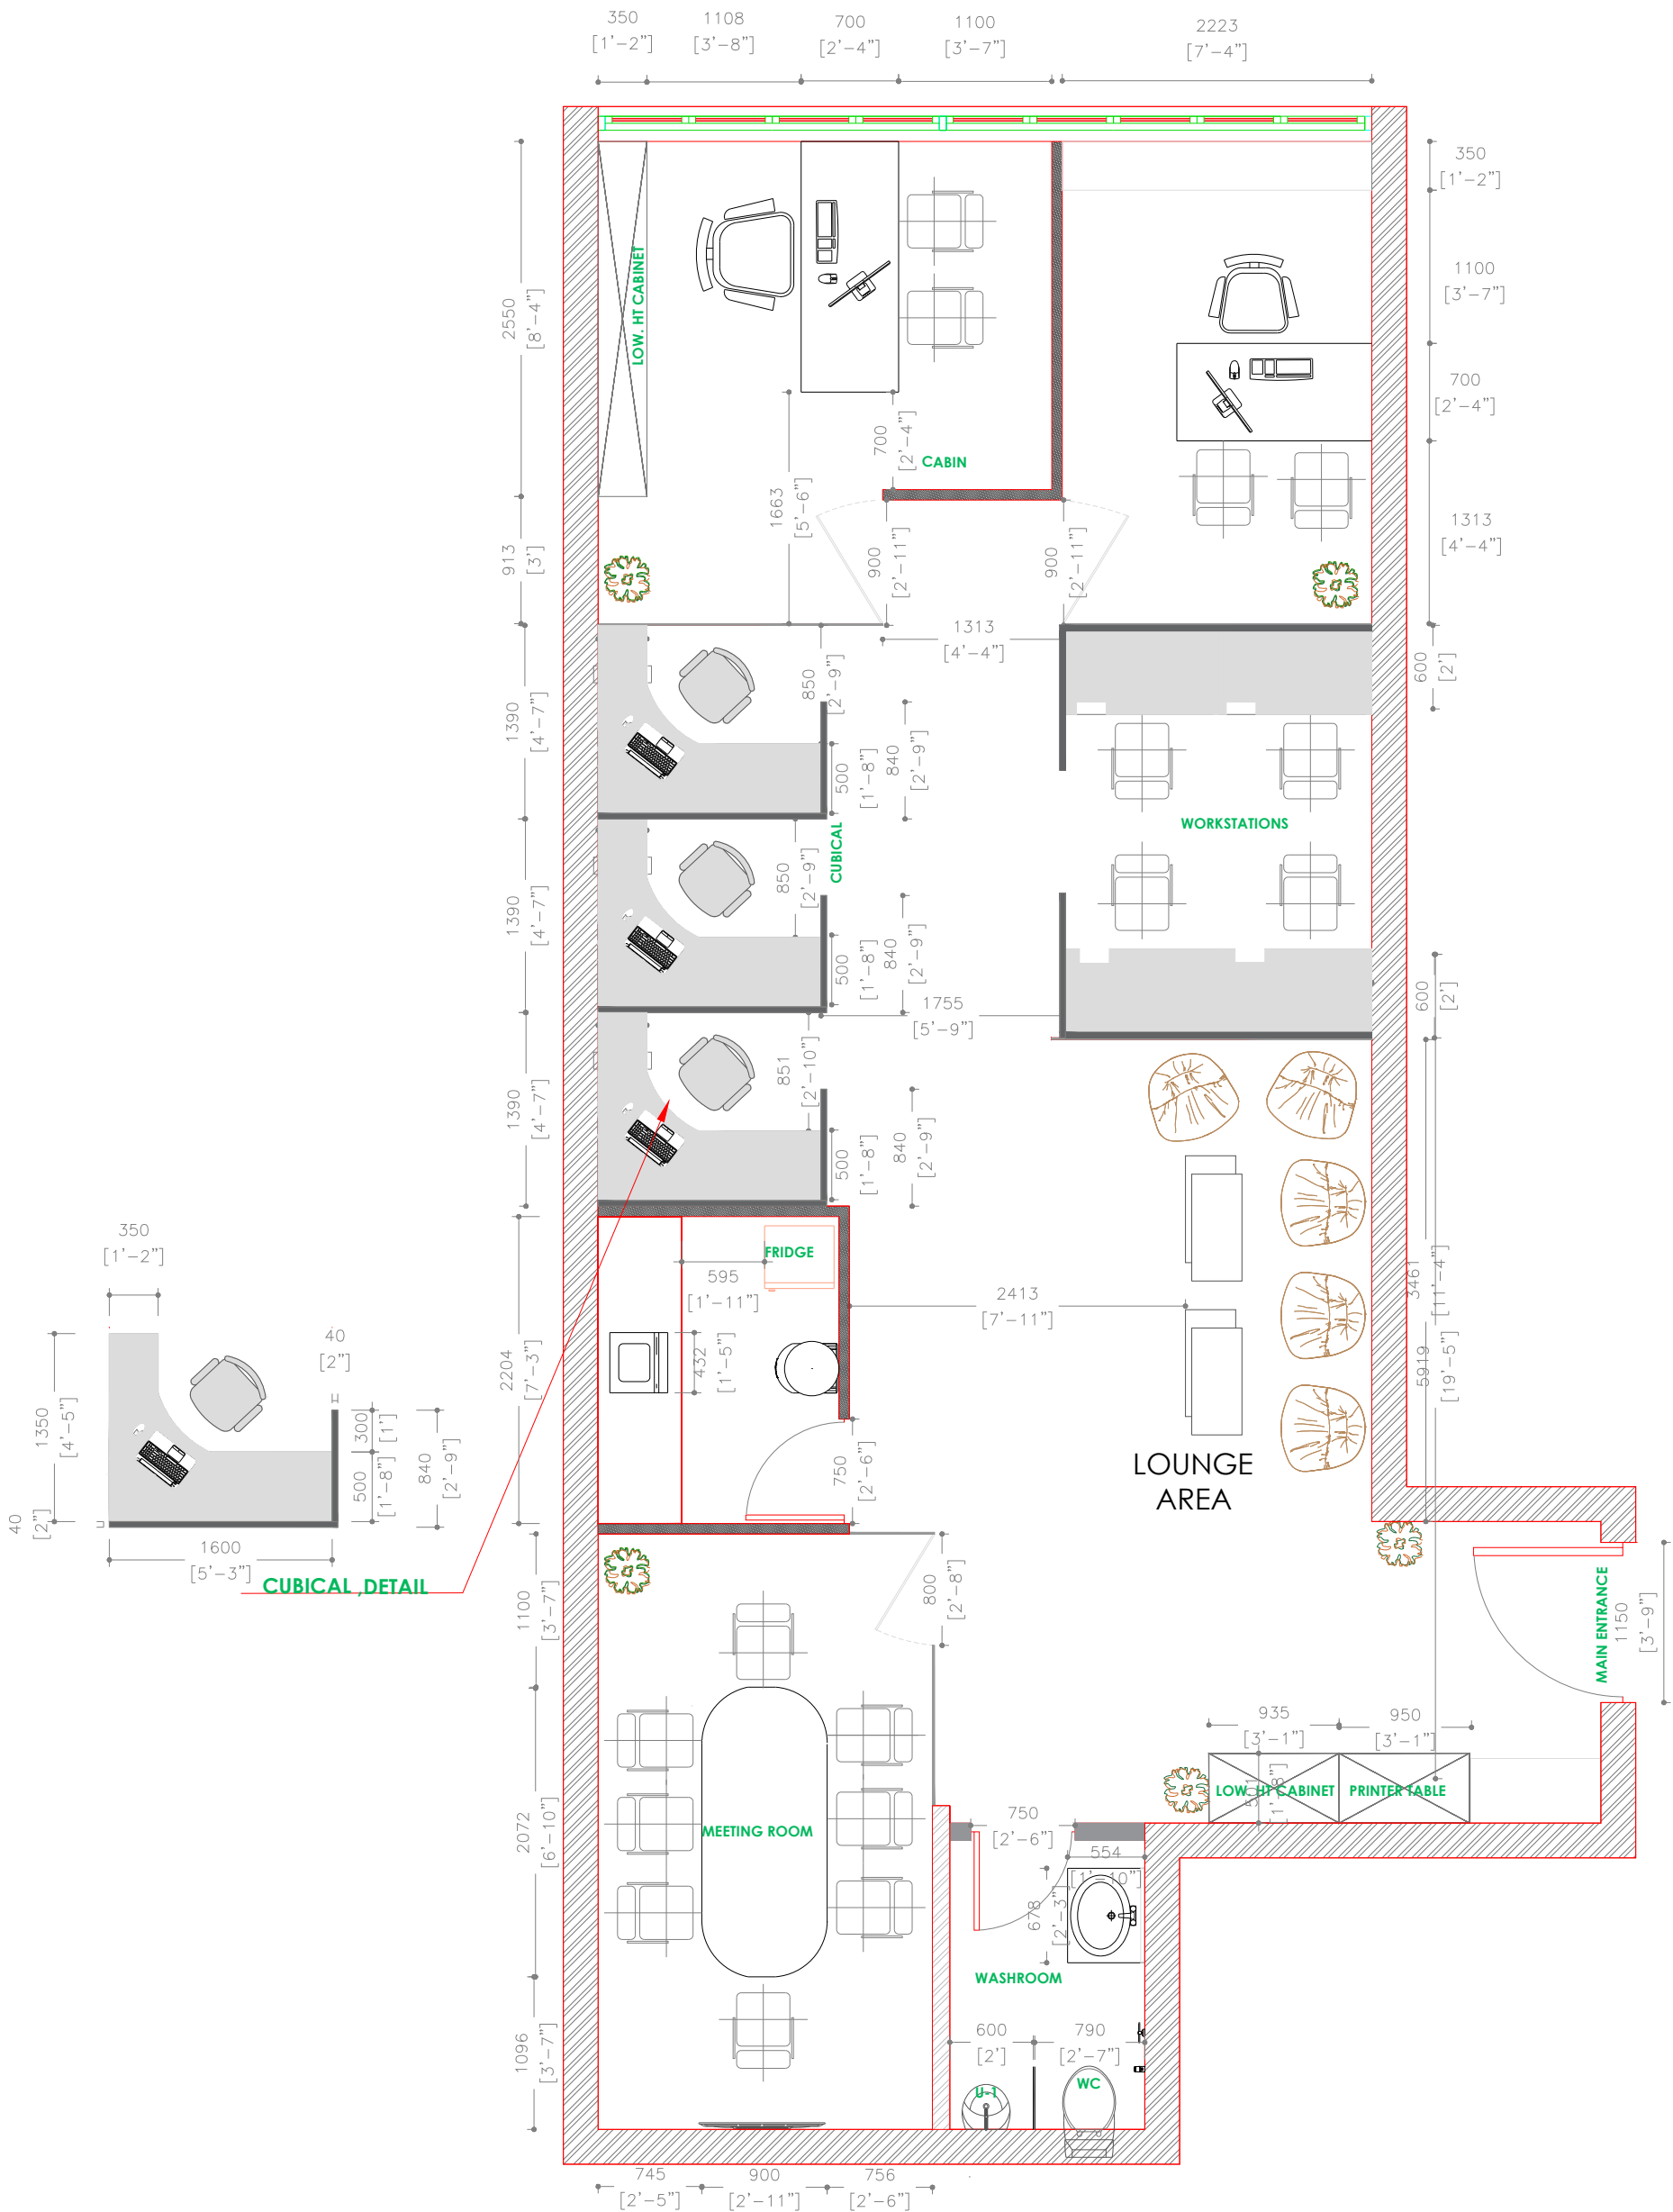

Note: All DIMENSIONS IN MM  
Note: All dimensions to be checked on site

DRY PARTITION =  
GLASS PARTITION =



| PROJECT DETAILS |                                            |                   | SITE DETAILS |                                  |                              | DRAWING DETAILS |                  |             | CLIENT | ARCHITECT                 |
|-----------------|--------------------------------------------|-------------------|--------------|----------------------------------|------------------------------|-----------------|------------------|-------------|--------|---------------------------|
| Project         | RENOVATION WORK                            | Floor             | -            | Dwg Status                       | FURNITURE SETTING-OUT LAYOUT | 10-03-2026      | ABHISHEK DWIVEDI | POOJA DAKSH |        | BIRD ENGINEERING PVT LTD. |
| Site            | E-9 , 2RD FLOOR CP                         | Floor carpet Area | - 78.98 SQM  | Dwg Title                        | INTERNAL LAYOUT              |                 |                  |             |        |                           |
| Address         | E-9, Connaught House, CP, New Delhi, 11001 | B.O.Slab          | -            | Dwg No.                          | 4                            |                 |                  |             |        |                           |
| Channel P       | -                                          | B.O.Beam          | -            | Scale                            | Fit to paper                 |                 |                  |             |        |                           |
|                 |                                            | B.O.F.Ceiling     | -            | All the dimensions in millimeter |                              |                 |                  |             |        |                           |