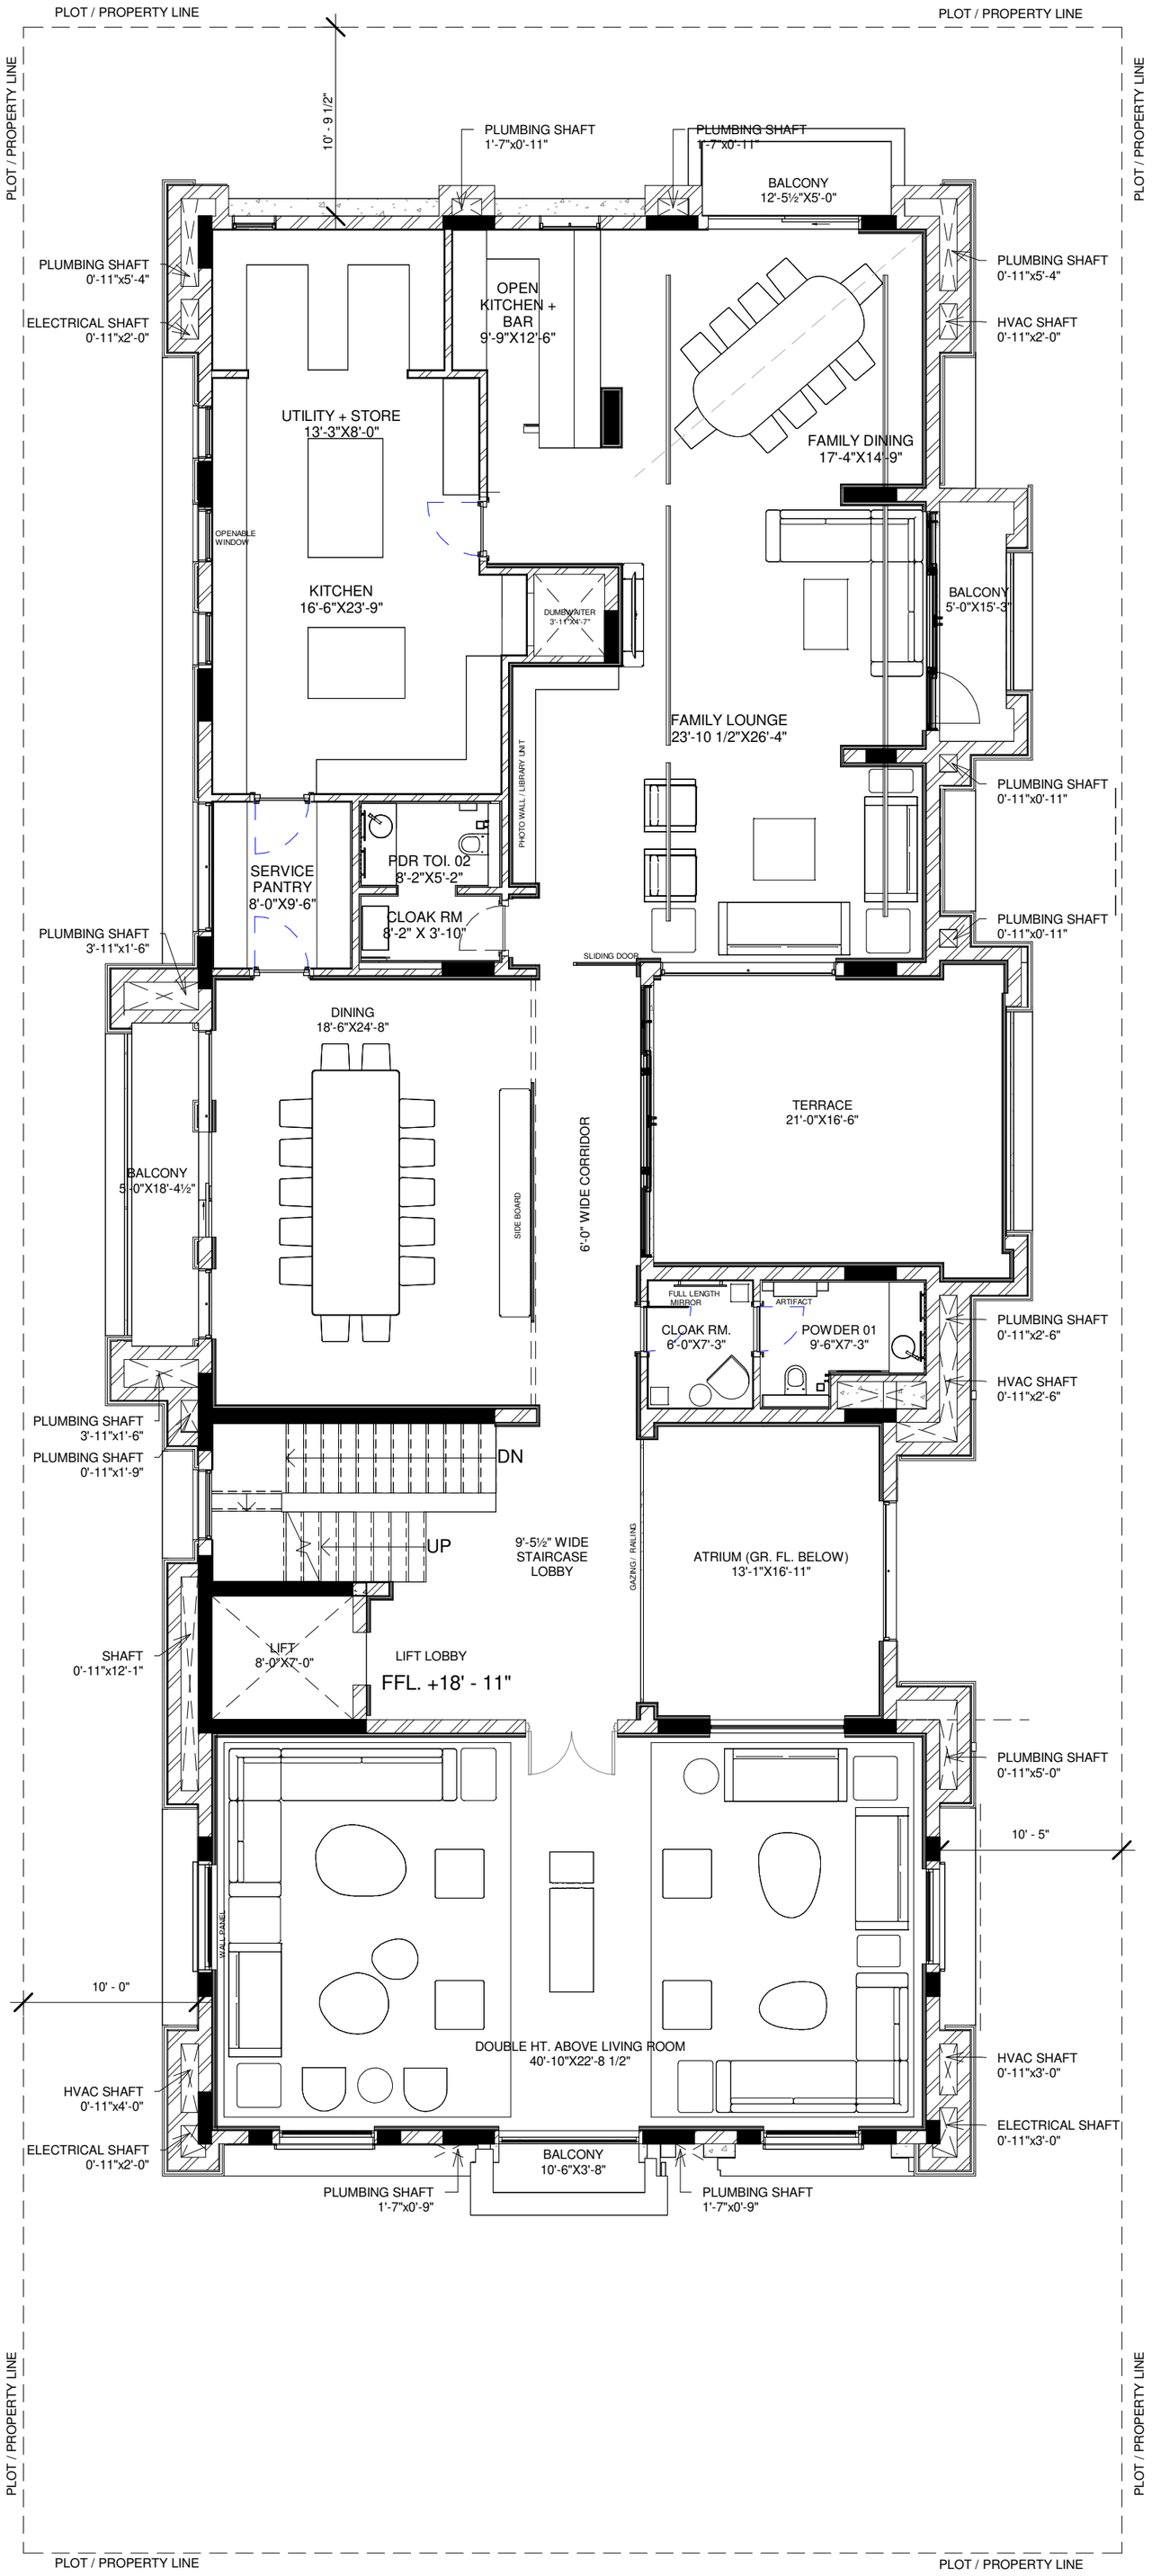

DOOR TYPE	CIVIL OPENING (BRICK TO BRICK)	LINTEL LVL	QTY
SD1	4730	2750	1
SD2	1830	2750	1
D1	1600	2750	1
D2	1118	2750	3
D3	965	2750	3

NOTE : DOOR LINTEL SHOULD BE AS PER BOTTOM OF CEILING OF LOWER CEILING WHICH IS 9'-0"

1 GROUND FLOOR LAYOUT
1/8" = 1'-0"

GENERAL NOTES

01) THIS DRAWING IS THE PROPERTY OF THE FABDEZINE ATELIER.
IT SHALL NOT BE COPIED REPRODUCED OR USED FOR ANY OTHER PURPOSE THAN SPECIFIED.
02) THIS DRAWING IS MEANT TO BE READ, NOT MEASURED.
03) ALL DIMENSIONS MUST BE CHECKED ON SITE AND DISCREPANCIES VERIFIED WITH THE ARCHITECT.
04) THIS DRAWING SHALL BE CO-ORDINATED WITH THE RELEVANT STRUCTURAL AND OTHER CONSULTANTS DRAWINGS.
05) ALL DIMENSIONS ARE IN FEET/INCH.

SPECIAL NOTES

1) IN CASE OF ANY DESCRIPENCY IN DIMENSIONS, STRUCTURAL DRAWING TO BE FOLLOWED FOR SIZES AND ARCHITECT TO BE INFORMED
2) SECTIONS TO BE USED FOR THE REFERENCE OF BUILDING HEIGHT ONLY.
3) ALL SLAB THICKNESS, RCC WALLS, RETAINING WALLS, SHEAR WALLS, RAFT, BEAMS, COLUMNS, AND OTHER STRUCTURAL ELEMENTS SHOWN IN THIS DRAWING ARE NOTIONAL SIZES FOR ALL THESE ELEMENTS, THERE EXACT SIZES TO BE OBTAINED FROM STRUCTURAL DRAWING AND DETAILS.

R E V I S I O N

NO	DATE	PARTICULARS

P R O J E C T

BHATIA RESIDENCE

C-11 VASANT VIHAR

NORTH

T I T L E

GROUND FLOOR LAYOUT

. .

DRAWING NO. | REVISION

BR_ **ID-GF-01** | .

DATE	STATUS	TO	SETS
03/07/2025	.	SITE	MAIL & PRINT

DESIGN CONSULTANT
FABINTERIOR