
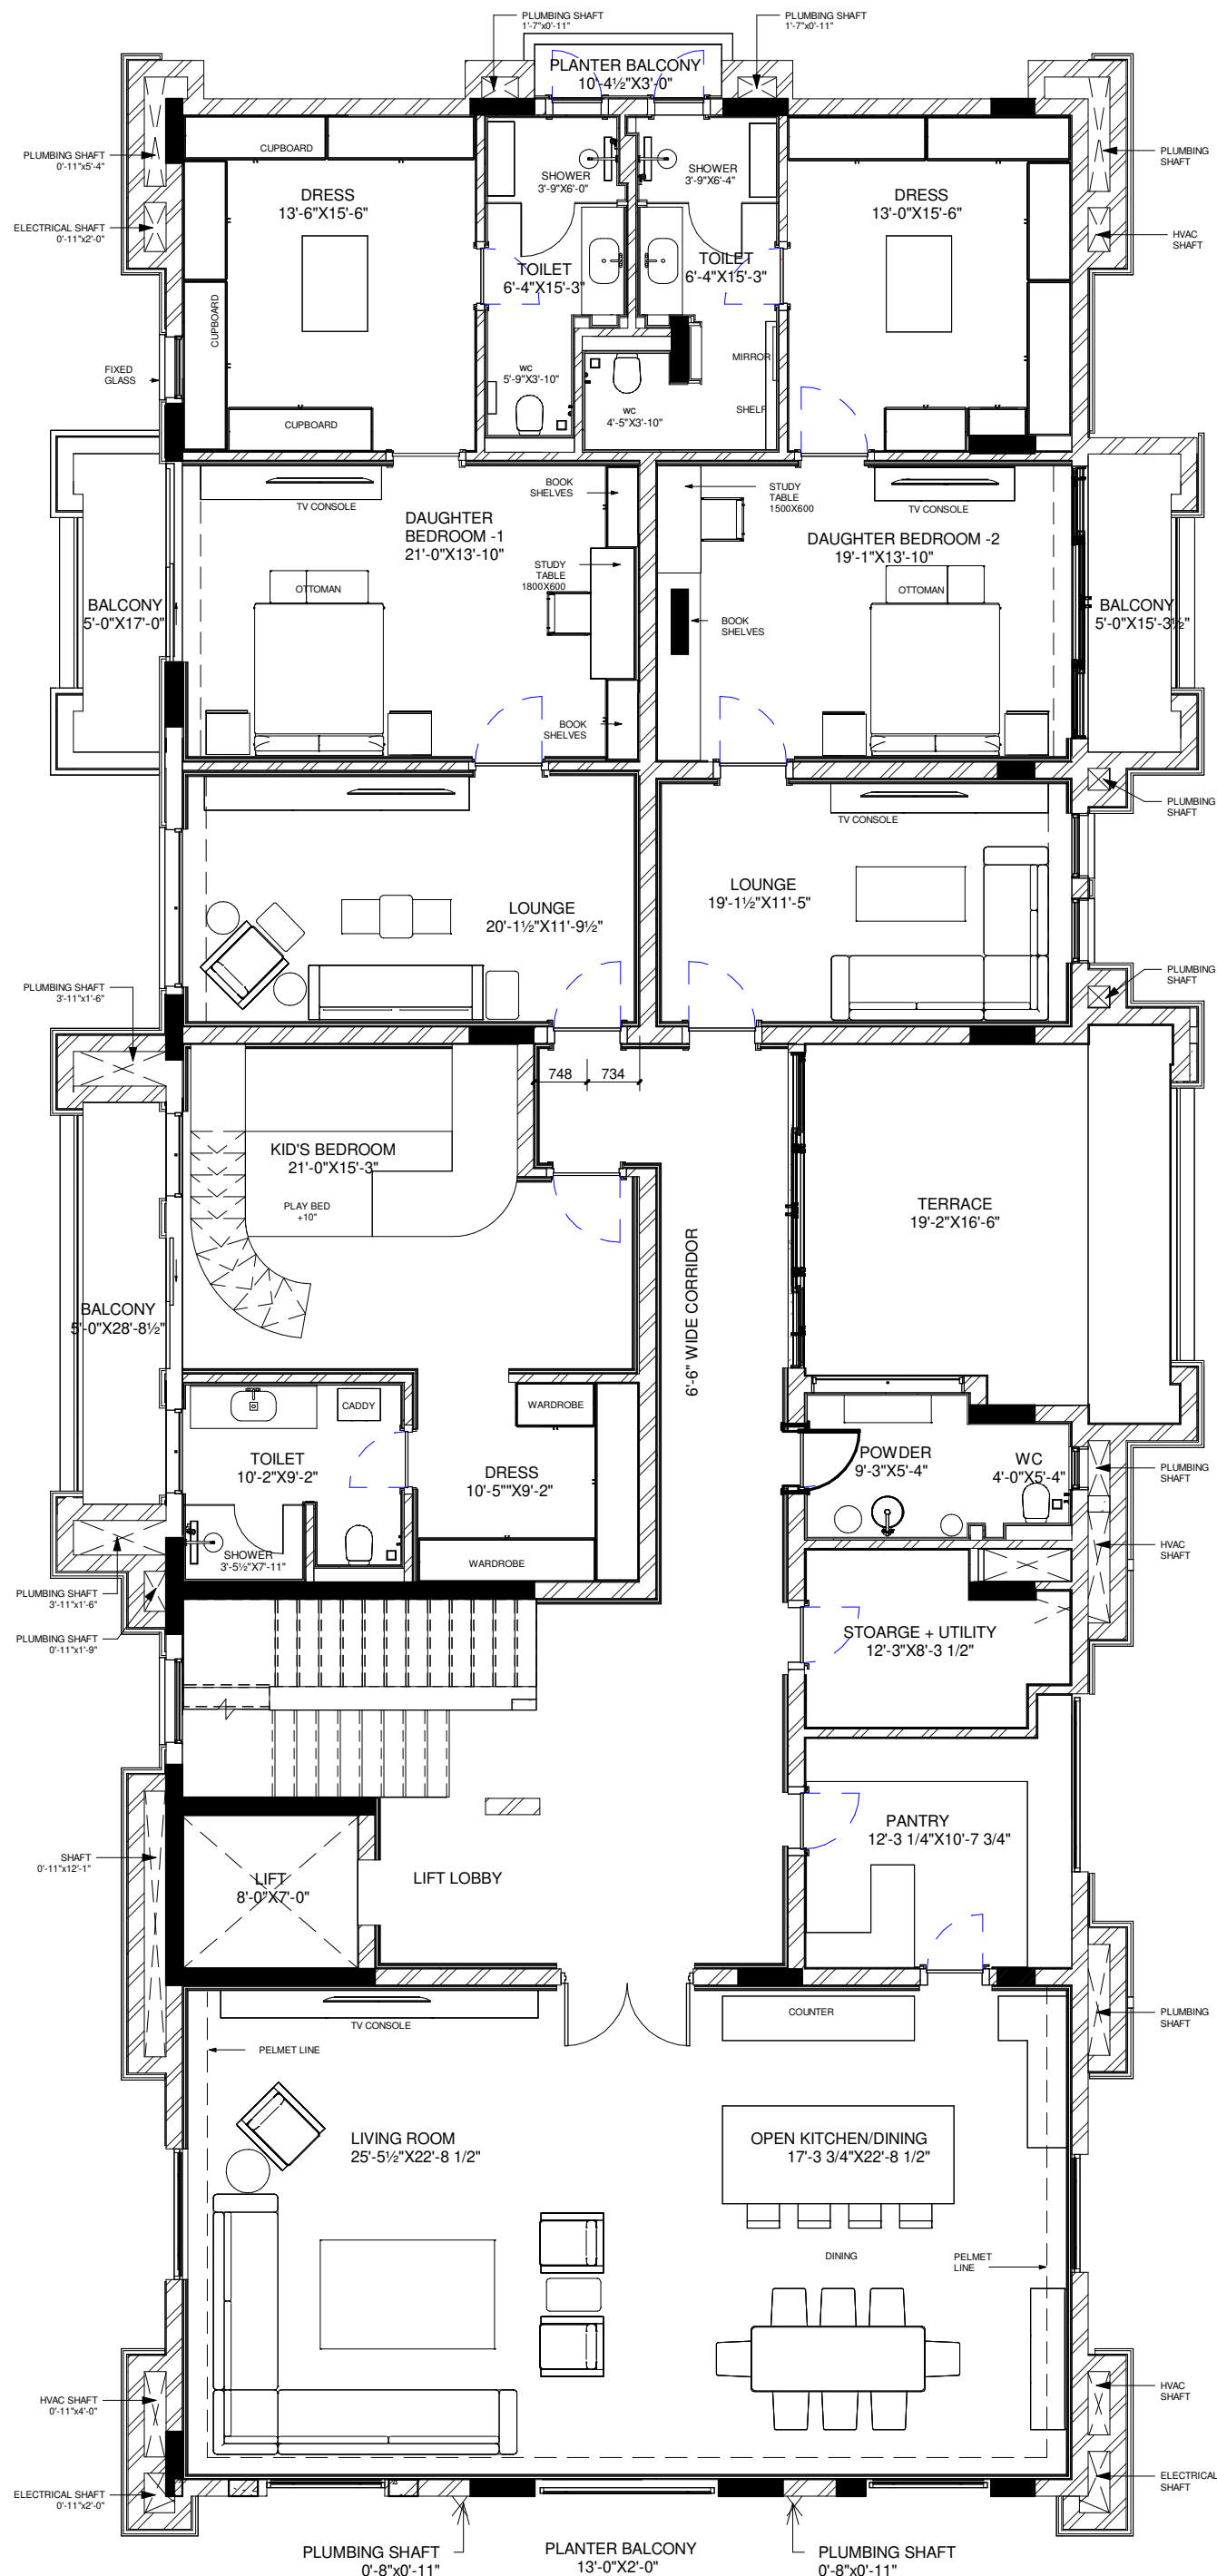


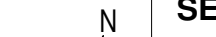

1 SECOND FLOOR LAYOUT
1/8" = 1'-0"

GENERAL NOTES		SPECIAL NOTES		R E V I S I O N			P R O J E C T		NORTH	T I T L E				 DESIGN CONSULTANT FABINTERIOR		
01) THIS DRAWING IS THE PROPERTY OF THE FABDEZINE ATELIER. IT SHALL NOT BE COPIED REPRODUCED OR USED FOR ANY OTHER PURPOSE THAN SPECIFIED. 02) THIS DRAWING IS MEANT TO BE READ, NOT MEASURED. 03) ALL DIMENSIONS MUST BE CHECKED ON SITE AND DISCREPANCIES VERIFIED WITH THE ARCHITECT. 04) THIS DRAWING SHALL BE CO-ORDINATED WITH THE RELEVANT STRUCTURAL AND OTHER CONSULTANTS DRAWINGS. 05) ALL DIMENSIONS ARE IN FEET/INCH.		1) IN CASE OF ANY DESCRIPENCY IN DIMENSIONS, STRUCTURAL DRAWING TO BE FOLLOWED FOR SIZES AND ARCHITECT TO BE INFORMED 2) SECTIONS TO BE USED FOR THE REFERENCE OF BUILDING HEIGHT ONLY. 3) ALL SLAB THICKNESS, RCC WALLS, RETAINING WALLS, SHEAR WALLS, RAFT, BEAMS, COLUMNS, AND OTHER STRUCTURAL ELEMENTS SHOWN IN THIS DRAWING ARE NOTIONAL SIZES FOR ALL THESE ELEMENTS, THERE EXACT SIZES TO BE OBTAINED FROM STRUCTURAL DRAWING AND DETAILS.		NO	DATE	PARTICULARS	BHATIA RESIDENCE C-11 VASANT VIHAR			SECOND FLOOR LAYOUT						
												DRAWING NO.			REVISION	
												BR_ ID-SF-101			R0	
												DATE			STATUS	
							03/07/2025		APPROVED		SITE	MAIL & PRINT				