


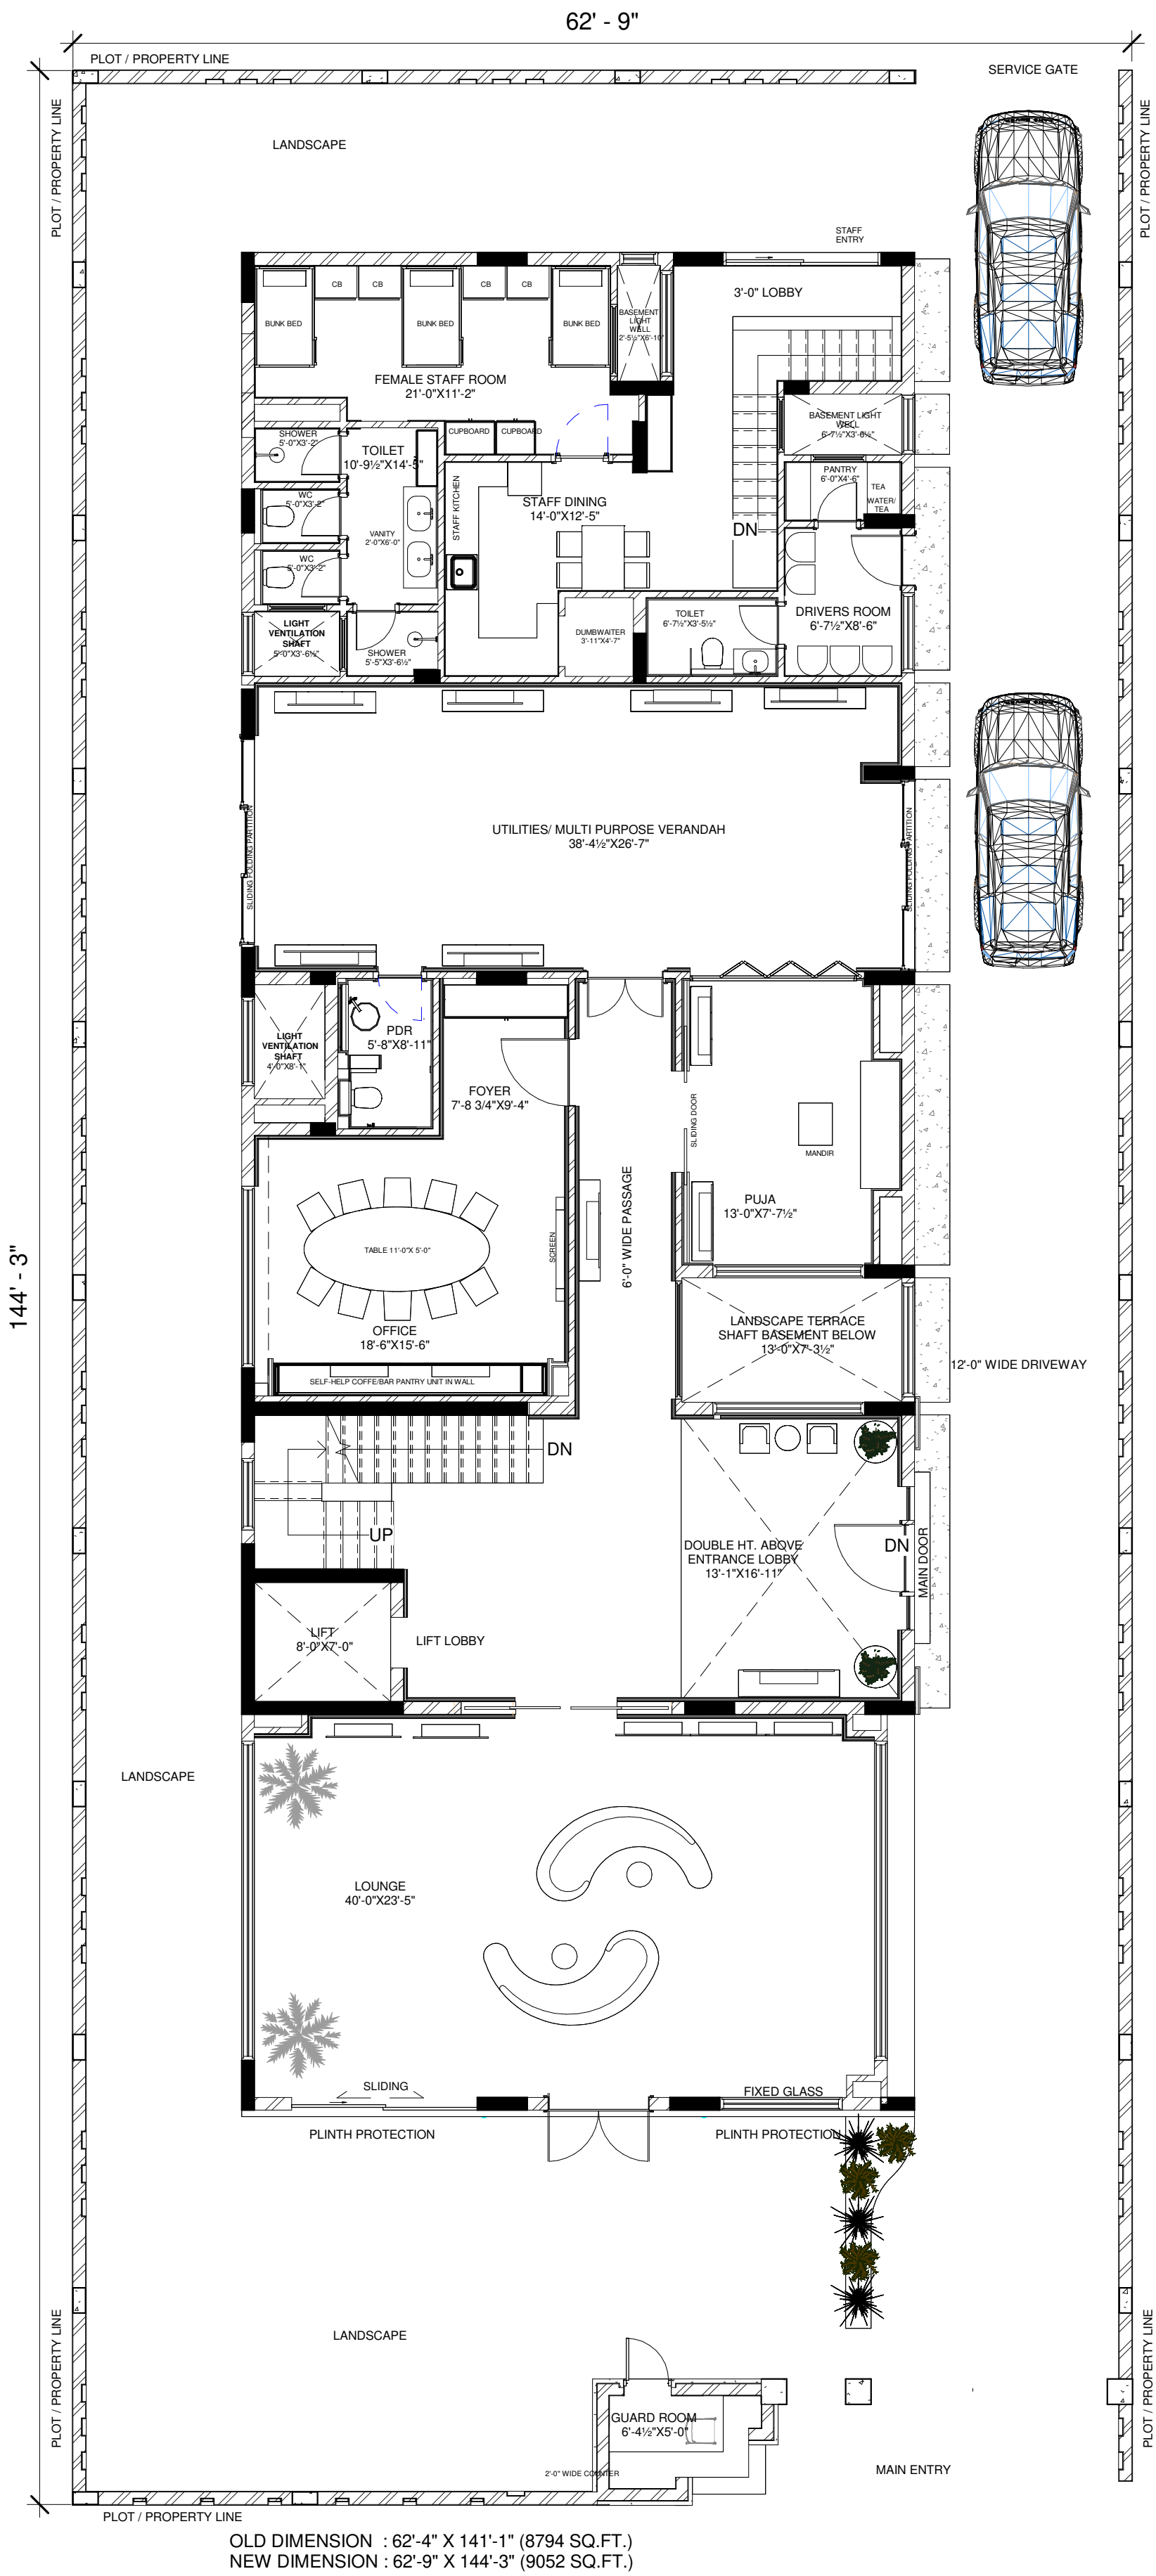

OLD DIMENSION : 62'-4" X 141'-1" (8794 SQ.FT.)
NEW DIMENSION : 62'-9" X 144'-3" (9052 SQ.FT.)

1 STILT FLOOR LAYOUT
1/8" = 1'-0"

DOOR TYPE	CIVIL OPENING (BRICK TO BRICK)	LINTEL LVL	QTY
SD1	3810	2413	1
SD2	1830	2261	1
SD3	3000	2261	1
D1	1575	2261	1
D2	1220	2261	1
D3A	965	2261	1
D3B	965	2197	1
D4	1118	2197	1
D5	838	2197	6

GENERAL NOTES	SPECIAL NOTES	R E V I S I O N			PROJECT	NORTH	TITLE						
01) THIS DRAWING IS THE PROPERTY OF THE FABDEZINE ATELIER. IT SHALL NOT BE COPIED REPRODUCED OR USED FOR ANY OTHER PURPOSE THAN SPECIFIED. 02) THIS DRAWING IS MEANT TO BE READ, NOT MEASURED. 03) ALL DIMENSIONS MUST BE CHECKED ON SITE AND DISCREPANCIES VERIFIED WITH THE ARCHITECT. 04) THIS DRAWING SHALL BE CO-ORDINATED WITH THE RELEVANT STRUCTURAL AND OTHER CONSULTANTS DRAWINGS. 05) ALL DIMENSIONS ARE IN FEET/INCH.	1) IN CASE OF ANY DESCRIPENCY IN DIMENSIONS, STRUCTURAL DRAWING TO BE FOLLOWED FOR SIZES AND ARCHITECT TO BE INFORMED. 2) SECTIONS TO BE USED FOR THE REFERENCE OF BUILDING HEIGHT ONLY. 3) ALL SLAB THICKNESS, RCC WALLS, RETAINING WALLS, SHEAR WALLS, RAFT, BEAMS, COLUMNS, AND OTHER STRUCTURAL ELEMENTS SHOWN IN THIS DRAWING ARE NOTIONAL SIZES FOR ALL THESE ELEMENTS, THERE EXACT SIZES TO BE OBTAINED FROM STRUCTURAL DRAWING AND DETAILS.	NO	DATE	PARTICULARS	BHATIA RESIDENCE C-11 VASANT VIHAR		STILT FLOOR LAYOUT .		REVISION				
											DRAWING NO.	R0	
									BR_		ID-ST-101		
									DATE		STATUS	TO	SETS
									03/07/2025		FOR APPROVAL	SITE	MAIL & PRINT