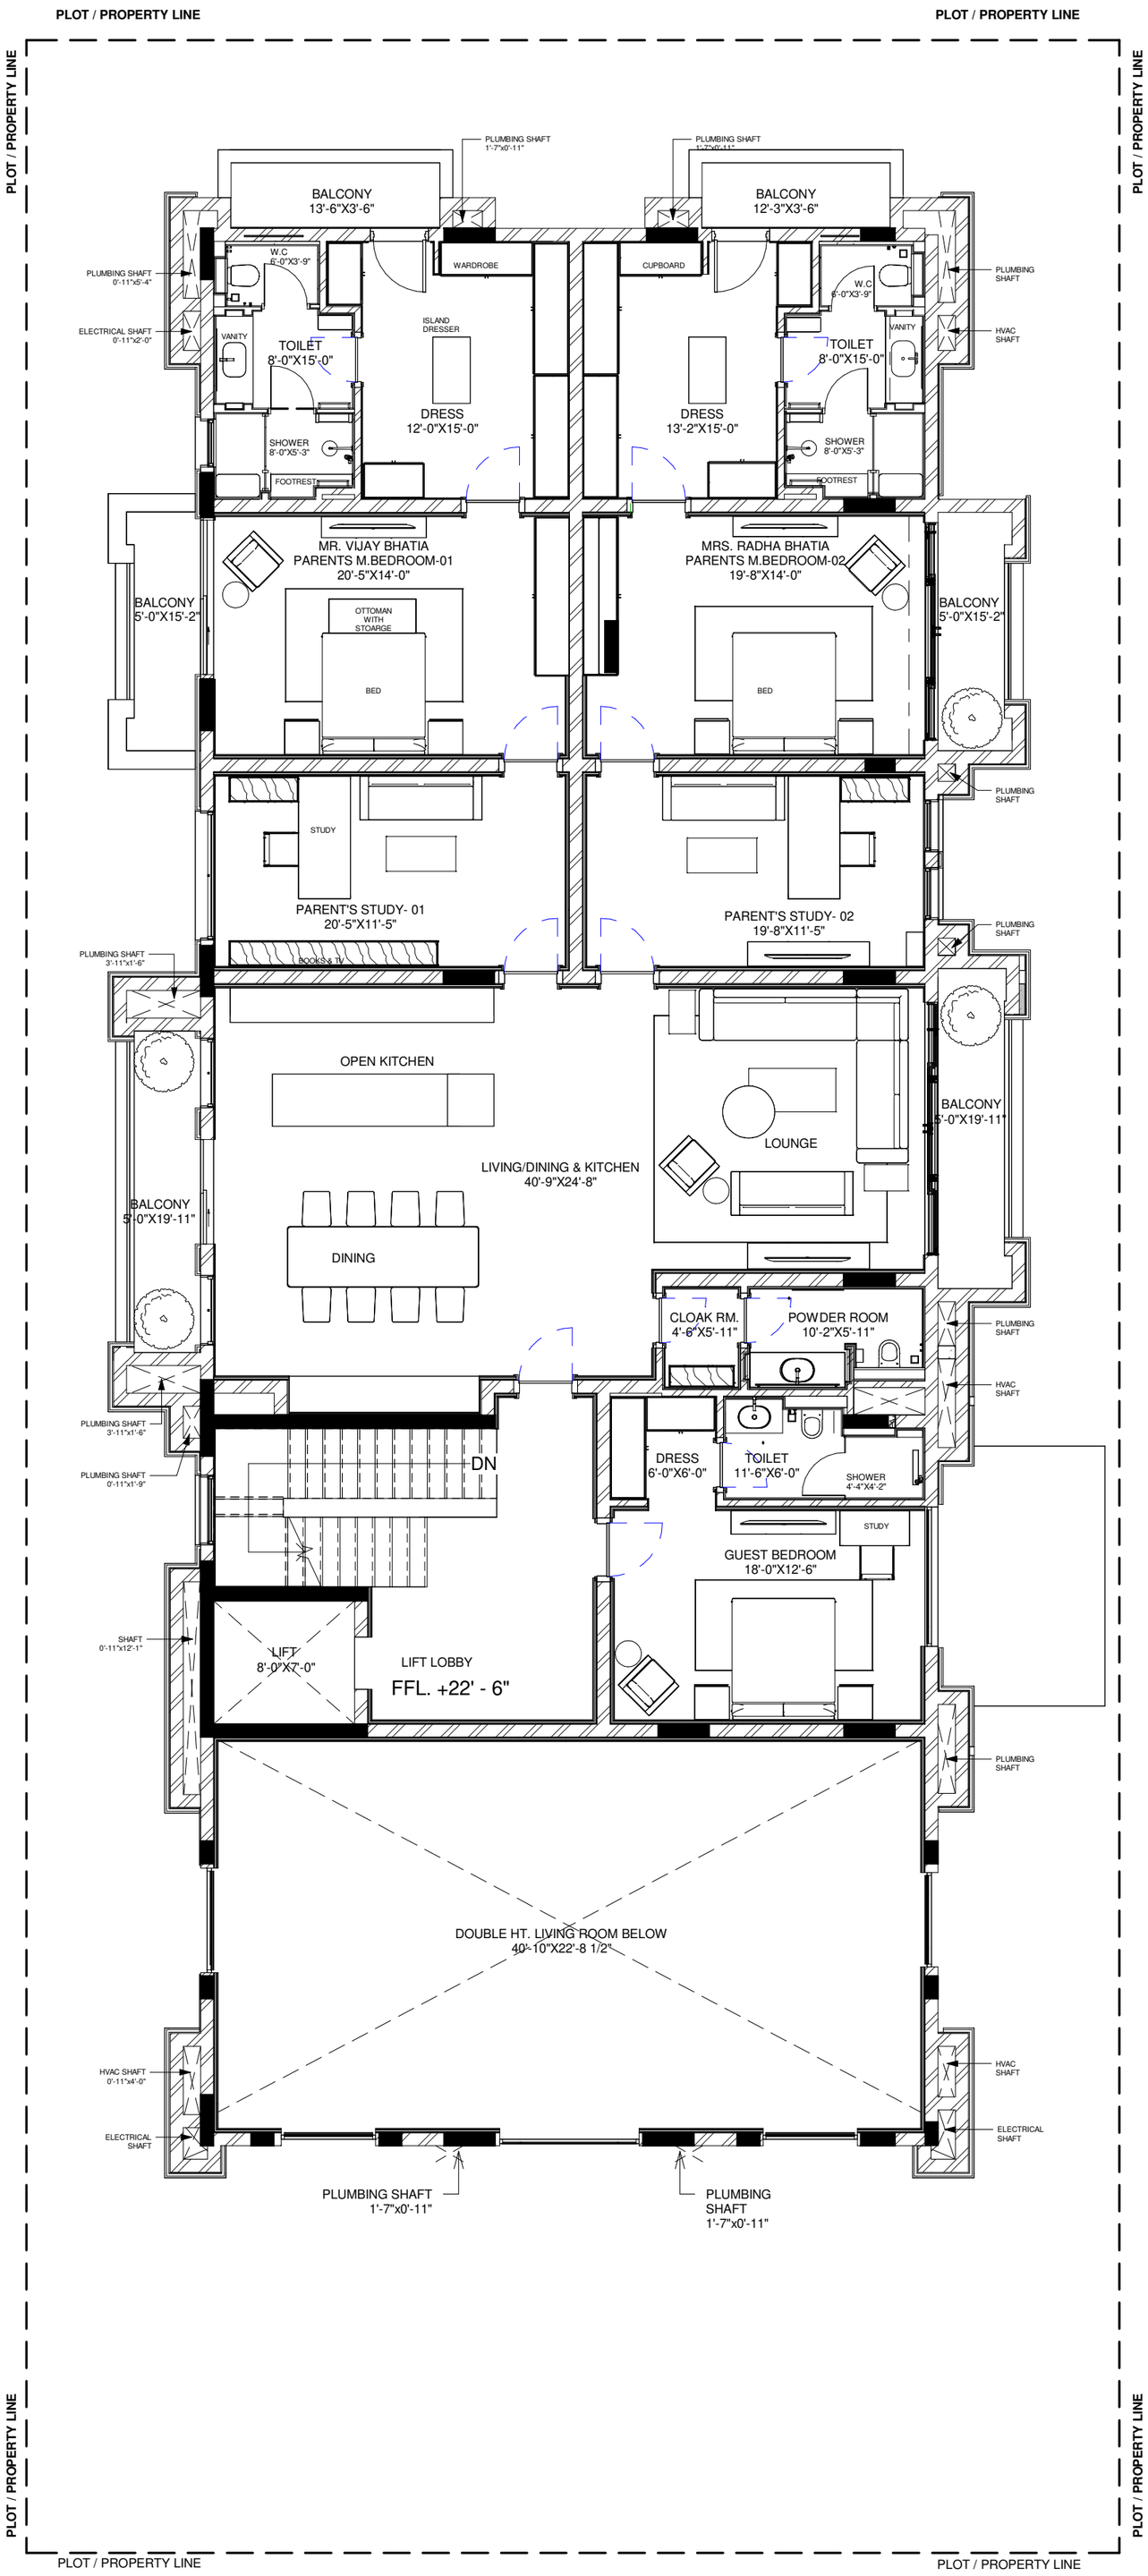


DOOR TYPE	CIVIL OPENING (BRICK TO BRICK)	LINTEL LVL	QTY
D1	1118	2750	8
D2	965	2750	5

1 FIRST FLOOR LAYOUT
1/8" = 1'-0"

GENERAL NOTES

01) THIS DRAWING IS THE PROPERTY OF THE FABDEZINE ATELIER.
IT SHALL NOT BE COPIED REPRODUCED OR USED FOR ANY OTHER PURPOSE THAN SPECIFIED.
02) THIS DRAWING IS MEANT TO BE READ, NOT MEASURED.
03) ALL DIMENSIONS MUST BE CHECKED ON SITE AND DISCREPANCIES VERIFIED WITH THE ARCHITECT.
04) THIS DRAWING SHALL BE CO-ORDINATED WITH THE RELEVANT STRUCTURAL AND OTHER CONSULTANTS DRAWINGS.
05) ALL DIMENSIONS ARE IN FEET/INCH.

SPECIAL NOTES

1) IN CASE OF ANY DESCRIPENCY IN DIMENSIONS, STRUCTURAL DRAWING TO BE FOLLOWED FOR SIZES AND ARCHITECT TO BE INFORMED
2) SECTIONS TO BE USED FOR THE REFERENCE OF BUILDING HEIGHT ONLY.
3) ALL SLAB THICKNESS, RCC WALLS, RETAINING WALLS, SHEAR WALLS, RAFT, BEAMS, COLUMNS, AND OTHER STRUCTURAL ELEMENTS SHOWN IN THIS DRAWING ARE NOTIONAL SIZES FOR ALL THESE ELEMENTS, THERE EXACT SIZES TO BE OBTAINED FROM STRUCTURAL DRAWING AND DETAILS.

REVISION

NO	DATE	PARTICULARS

PROJECT

BHATIA RESIDENCE

C-11 VASANT VIHAR

NORTH

TITLE

FIRST FLOOR LAYOUT

DRAWING NO. BR_ **ID-FF-101**

REVISION R0

DATE	STATUS	TO	SETS
03/07/2025	**FOR APPROVAL**	SITE	MAIL & PRINT

DESIGN CONSULTANT
FABINTERIOR