


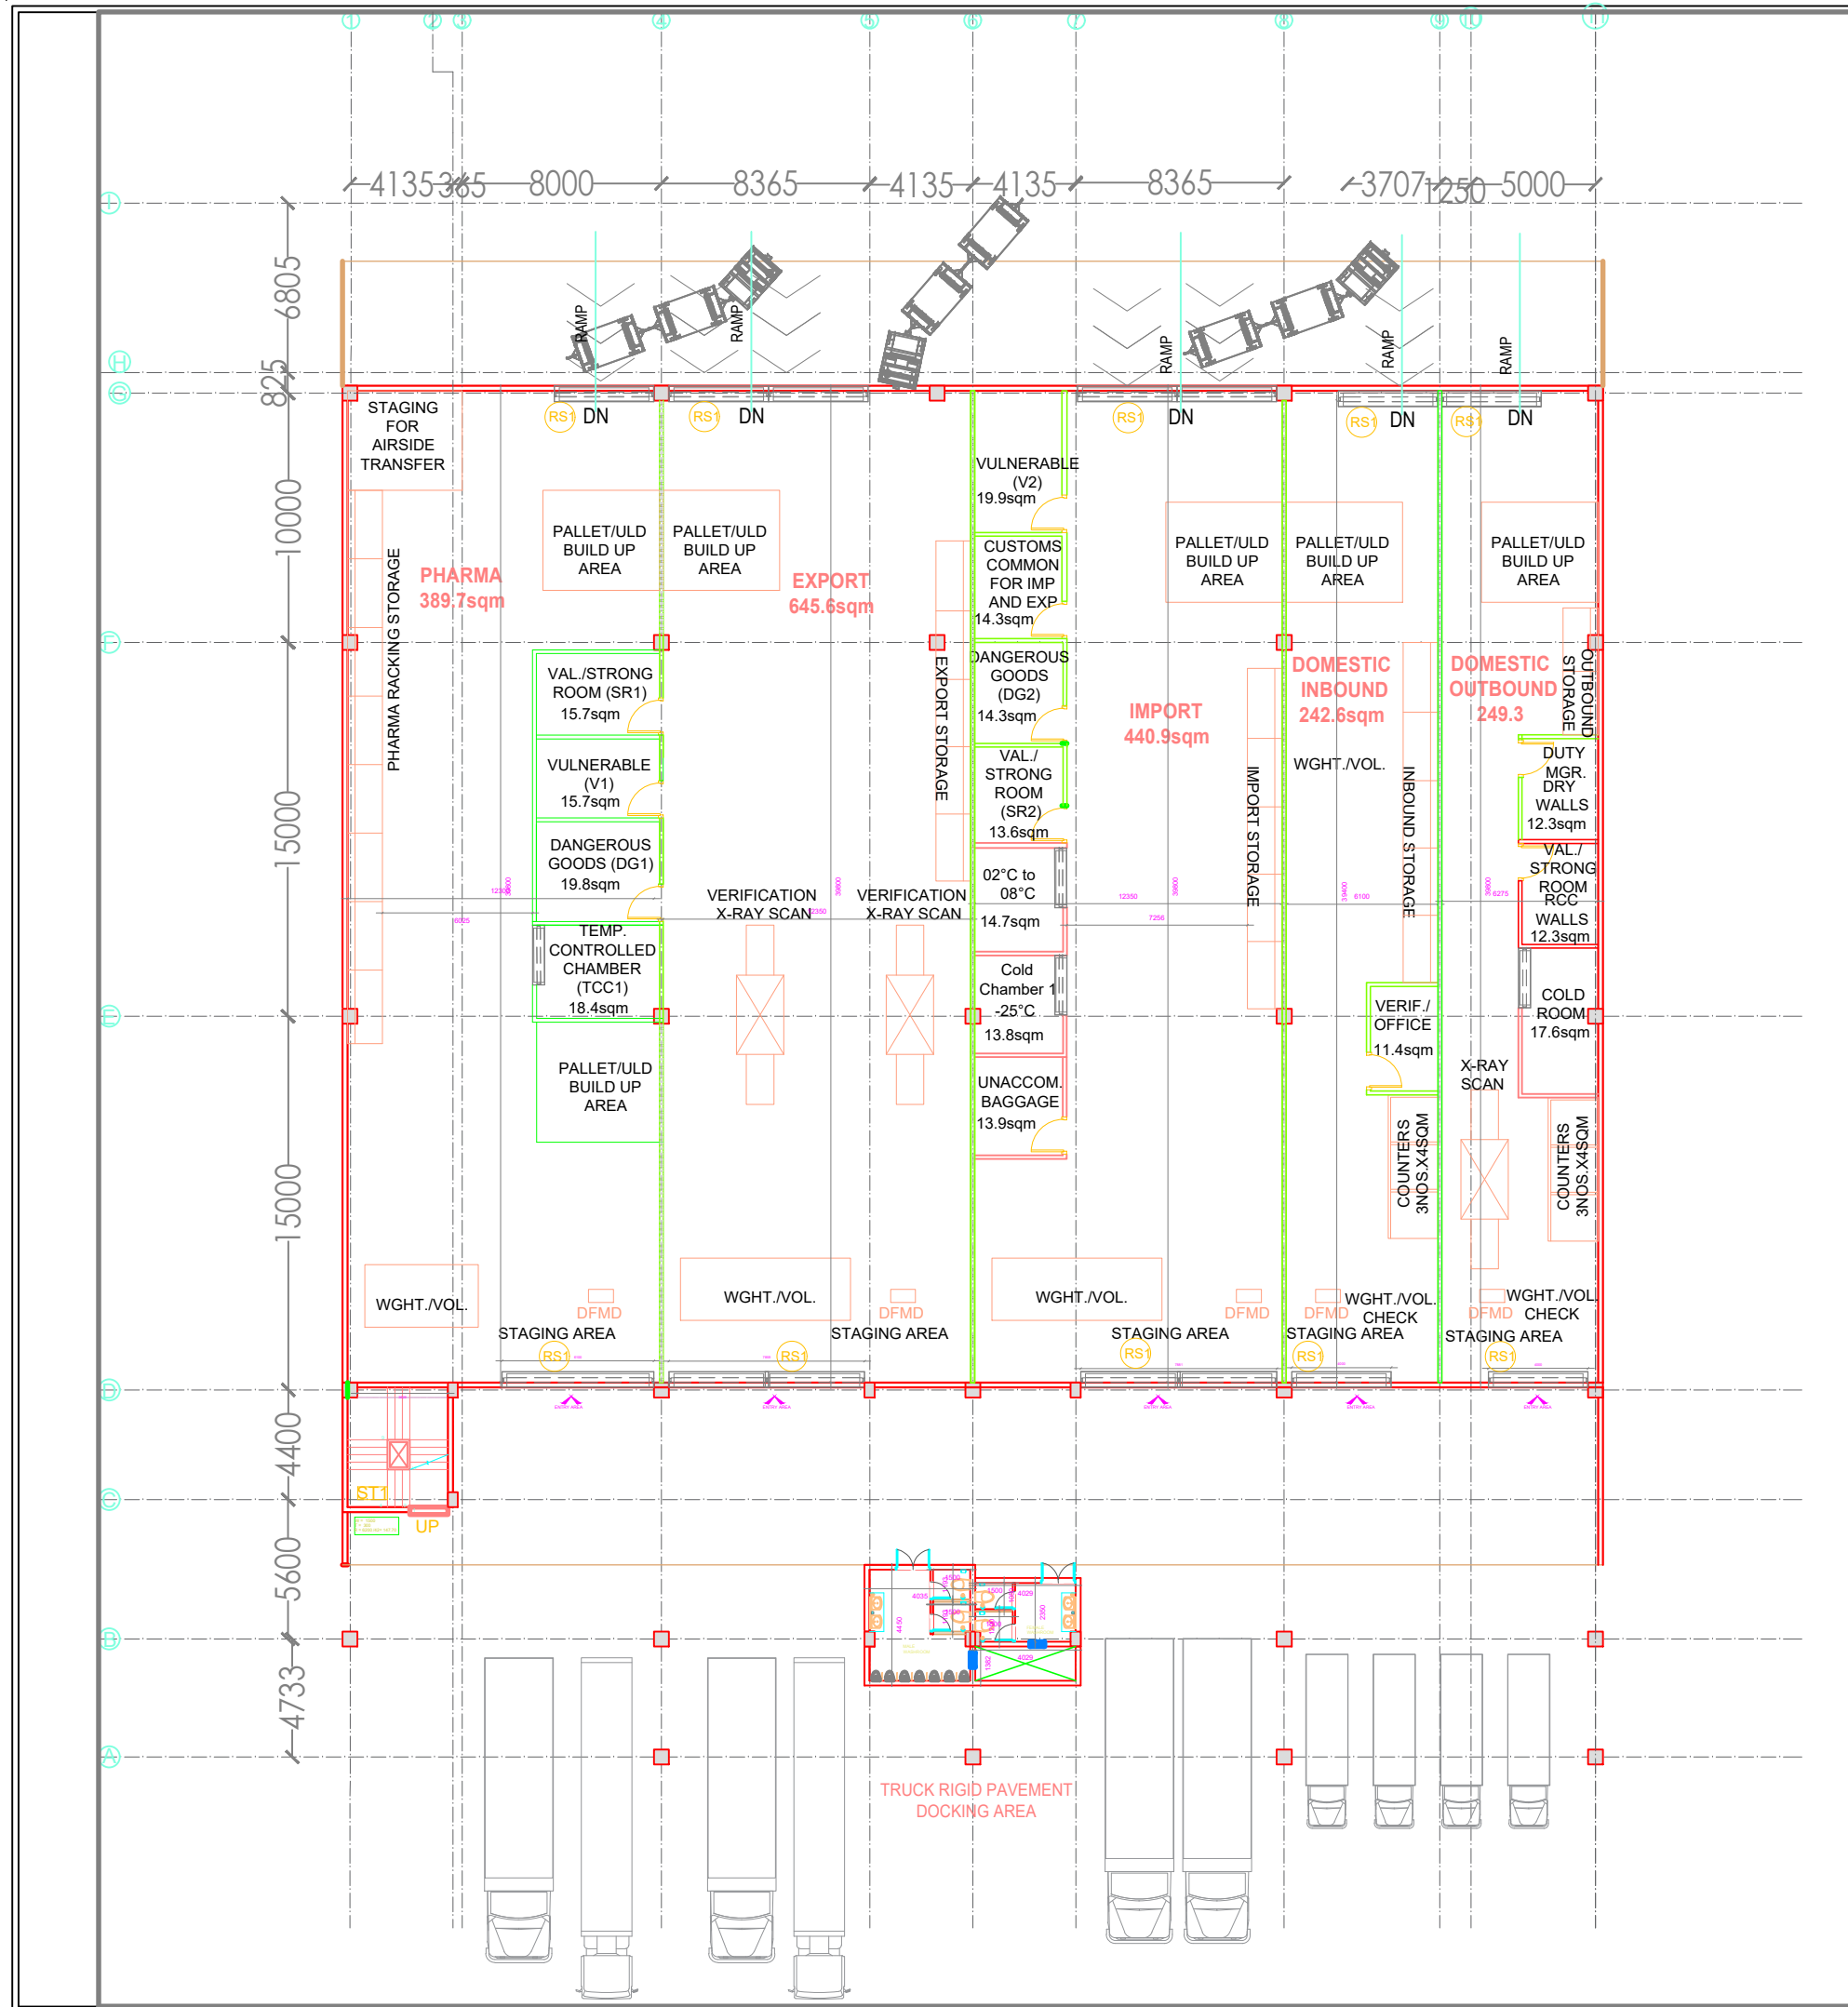

ARCHITECTURAL DRAWING

PROJECT NAME

PASSANDER TERMINAL
BUILDING & ALLIED WORKS
FOR NEW GREENFIELD
AIRPORT
DHOLERA, AHMEDABA
INDIA .

CLIENT



DHOLERA INTERNATIONAL
AIRPORT COMPANY LIMITED

CONTRACTOR



BIRD ENGINEERING
PVT. LTD.

8 IMT Manesar, Sector 5
Road, Manesar,
Gurugram, Haryana-122052

BUILDING NAME

CARGO TERMINAL BLOCK
(DOMESTIC CARGO)



ARCHITECT'S SIGN: AUTHORISED SIGN:

SHEET NAME :

GROUND FLOOR

DWG NO.: 101
DEALT BY: POOJA DAKSH
SCALE: 1:100
DATED: 11/06/2025